



S 60

Casement Window System

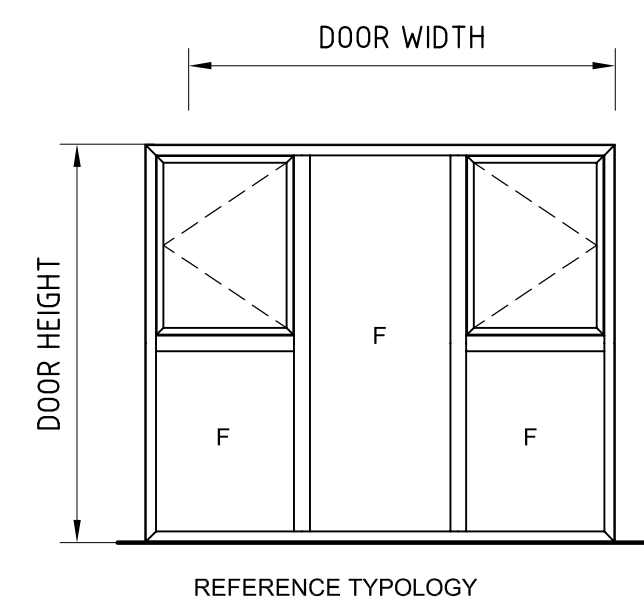


CERTIFICATIONS

- Air infiltration & Exfiltration (ASTM E283/E283M-19) 750 Pa
- Water Penetration (ASTM E331-00 Reapproved 2016) 600 Pa
- Wind Resistance Serviceability (ASTM E330/E330M-14) 1920 Pa
- Wind Resistance Safety (ASTM E330/E330M-14) 2880 Pa
- Maximum Panel Weight up to 130 kg
- Maximum Glass Thickness that can be accommodated is 53mm

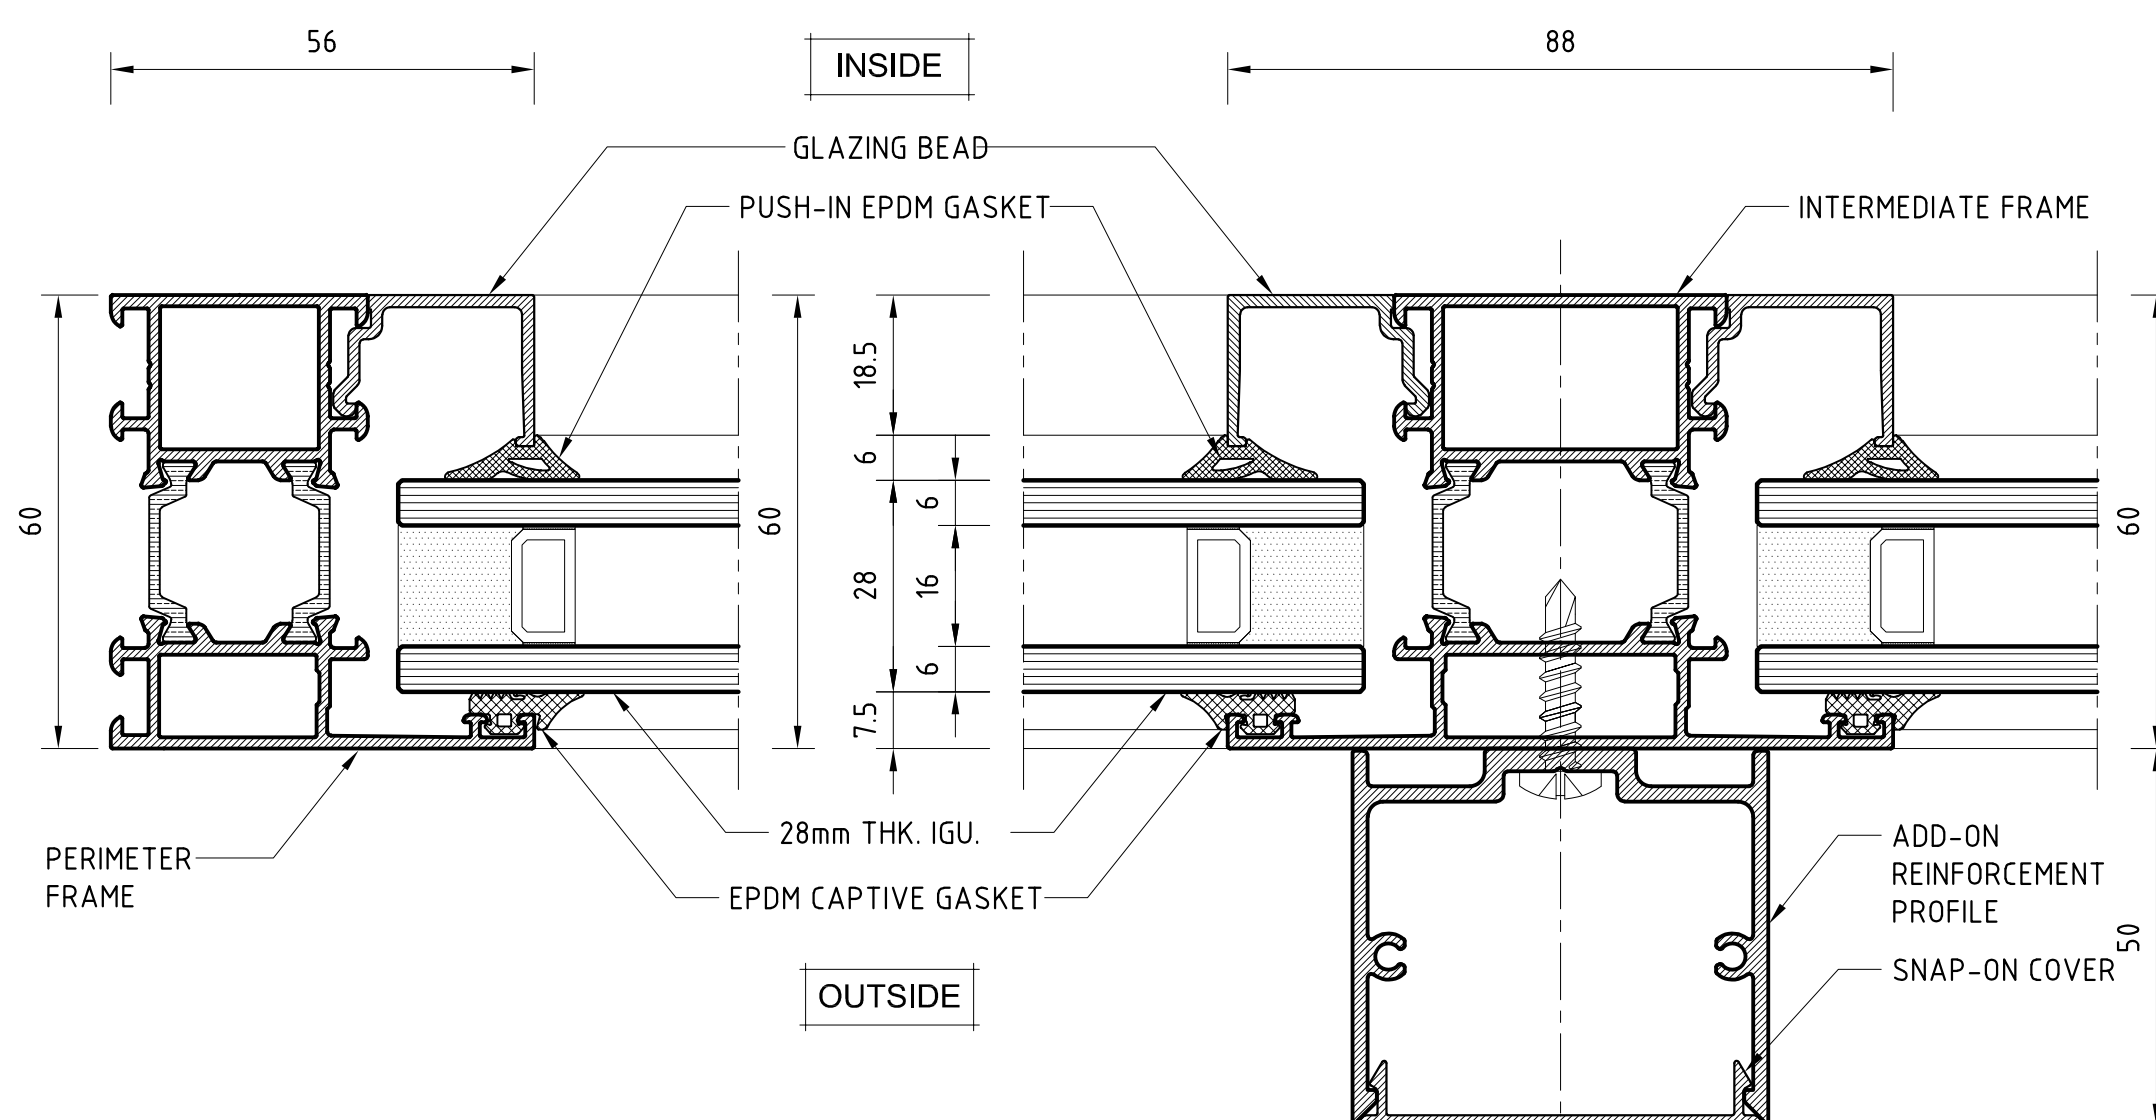


JAMB DETAIL

INTERMEDIATE DETAIL

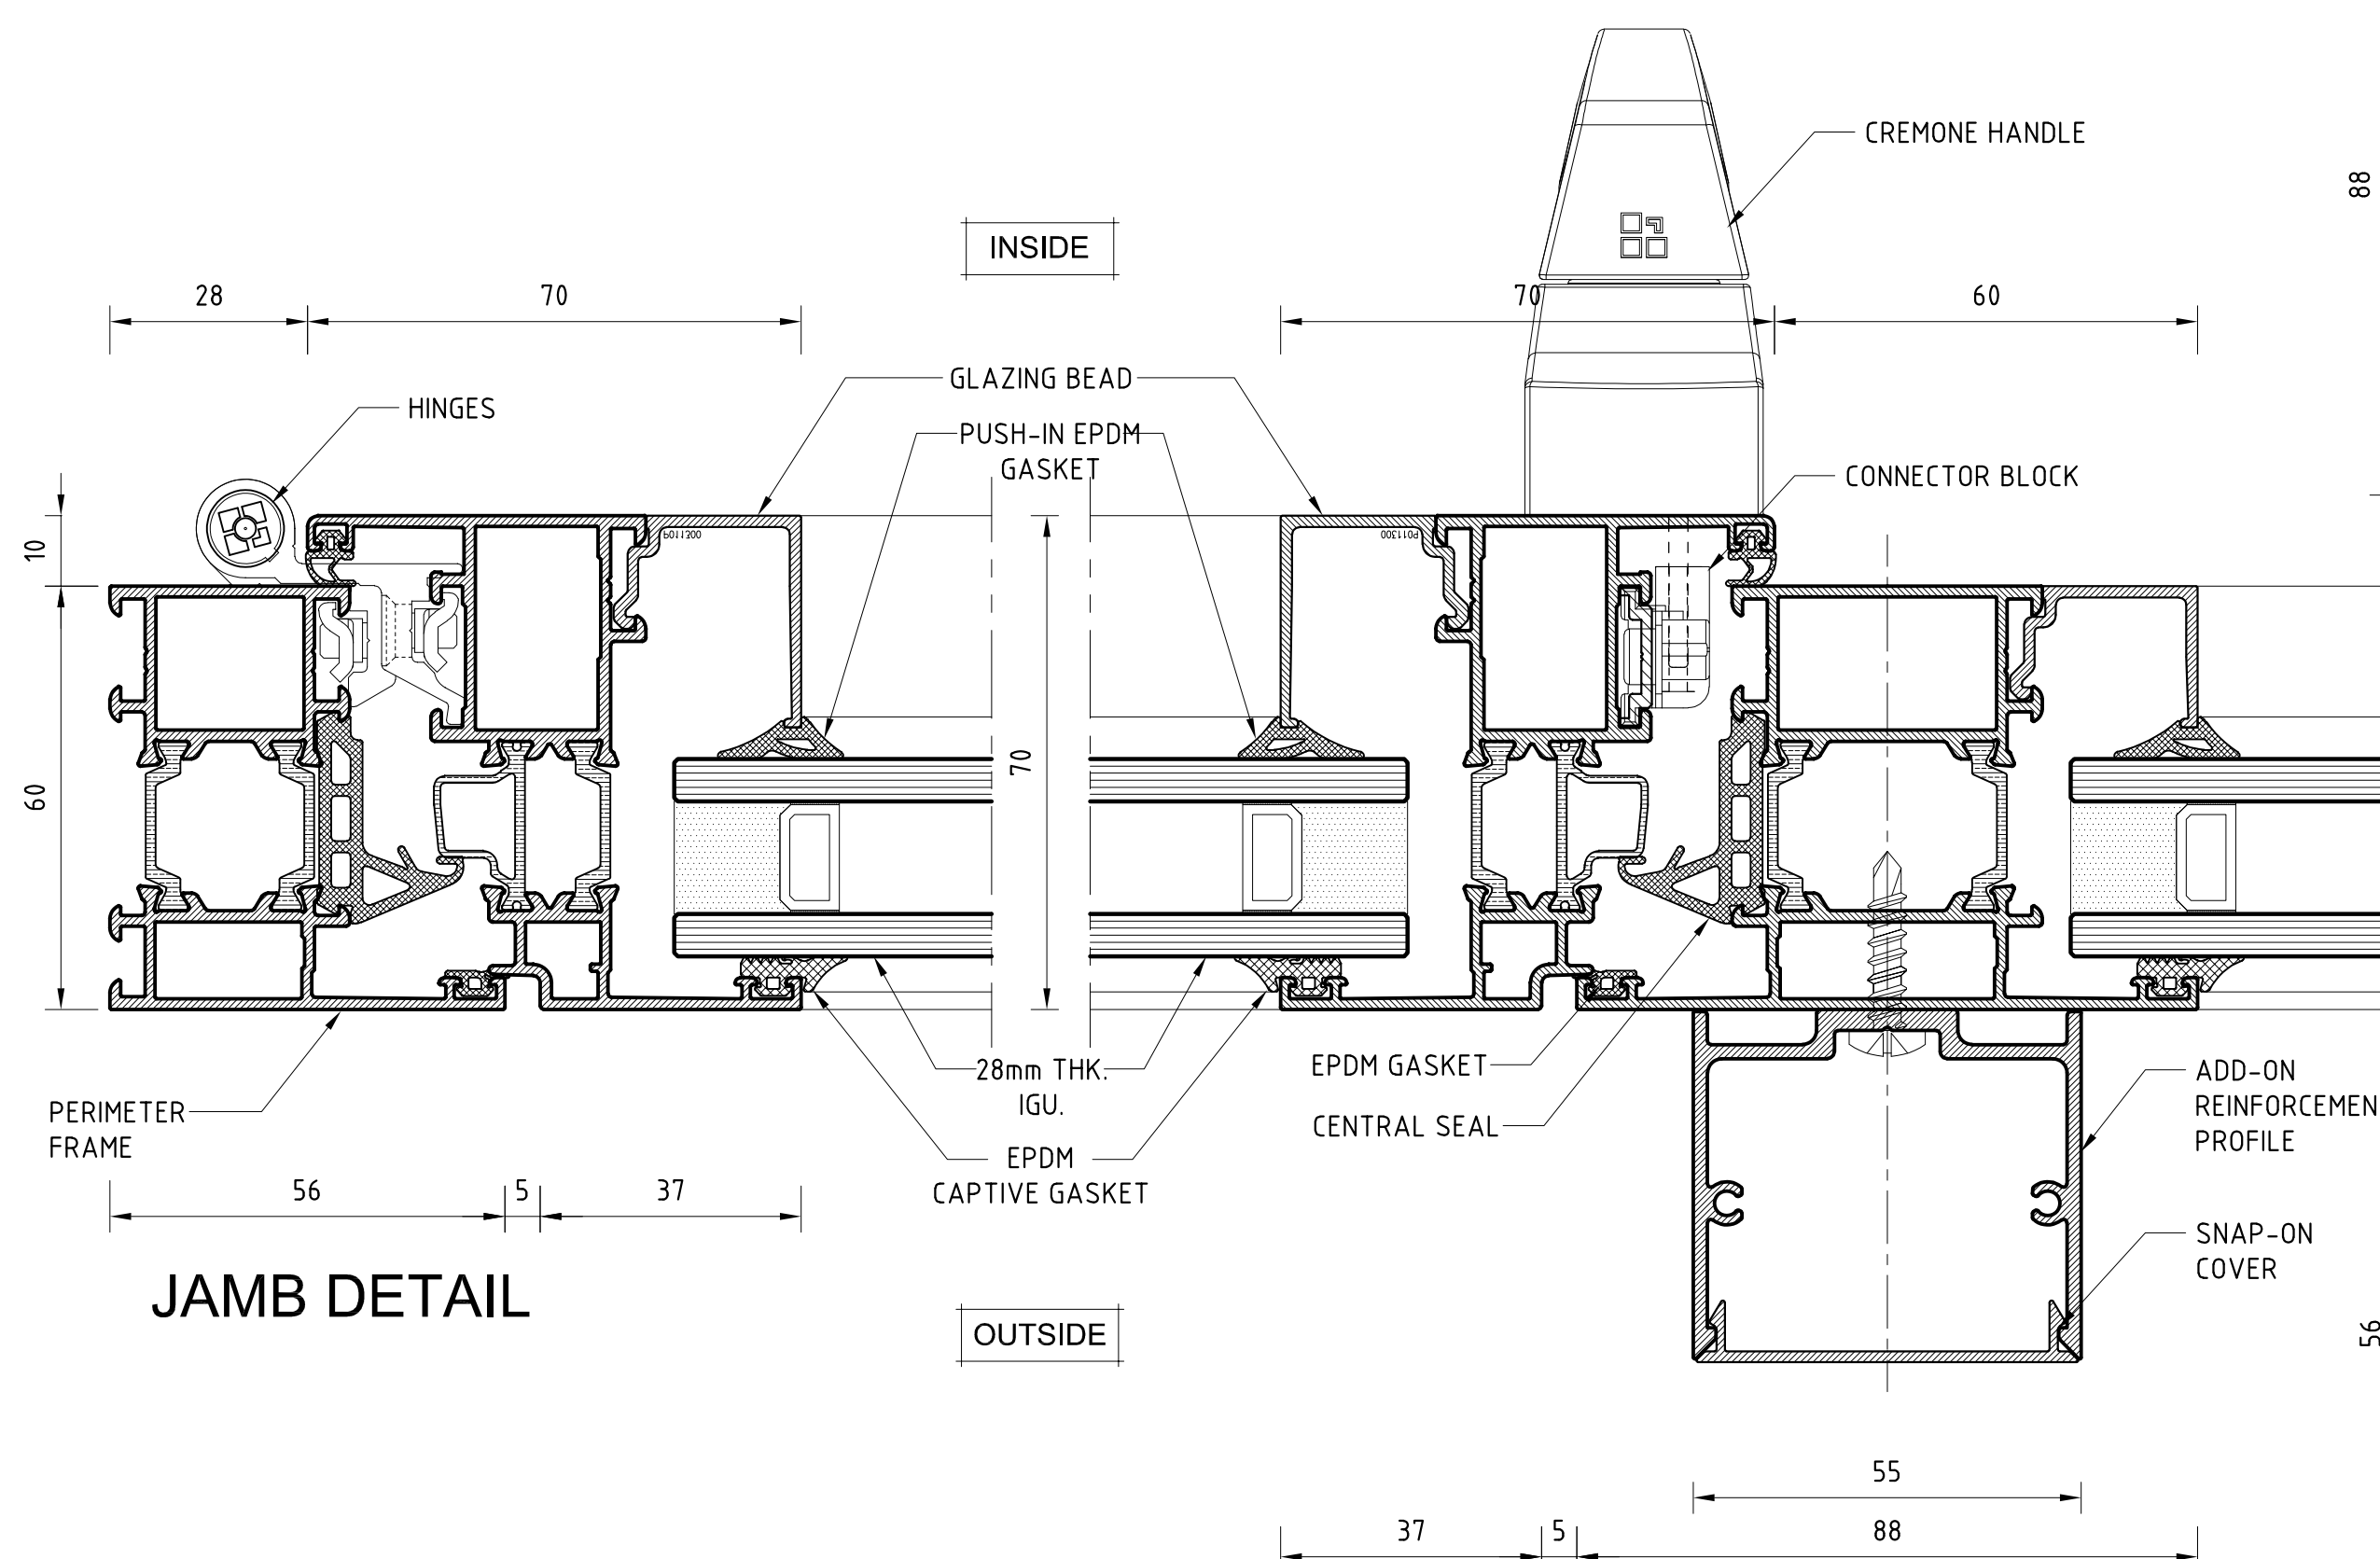


JAMB DETAIL


INTERMEDIATE DETAIL

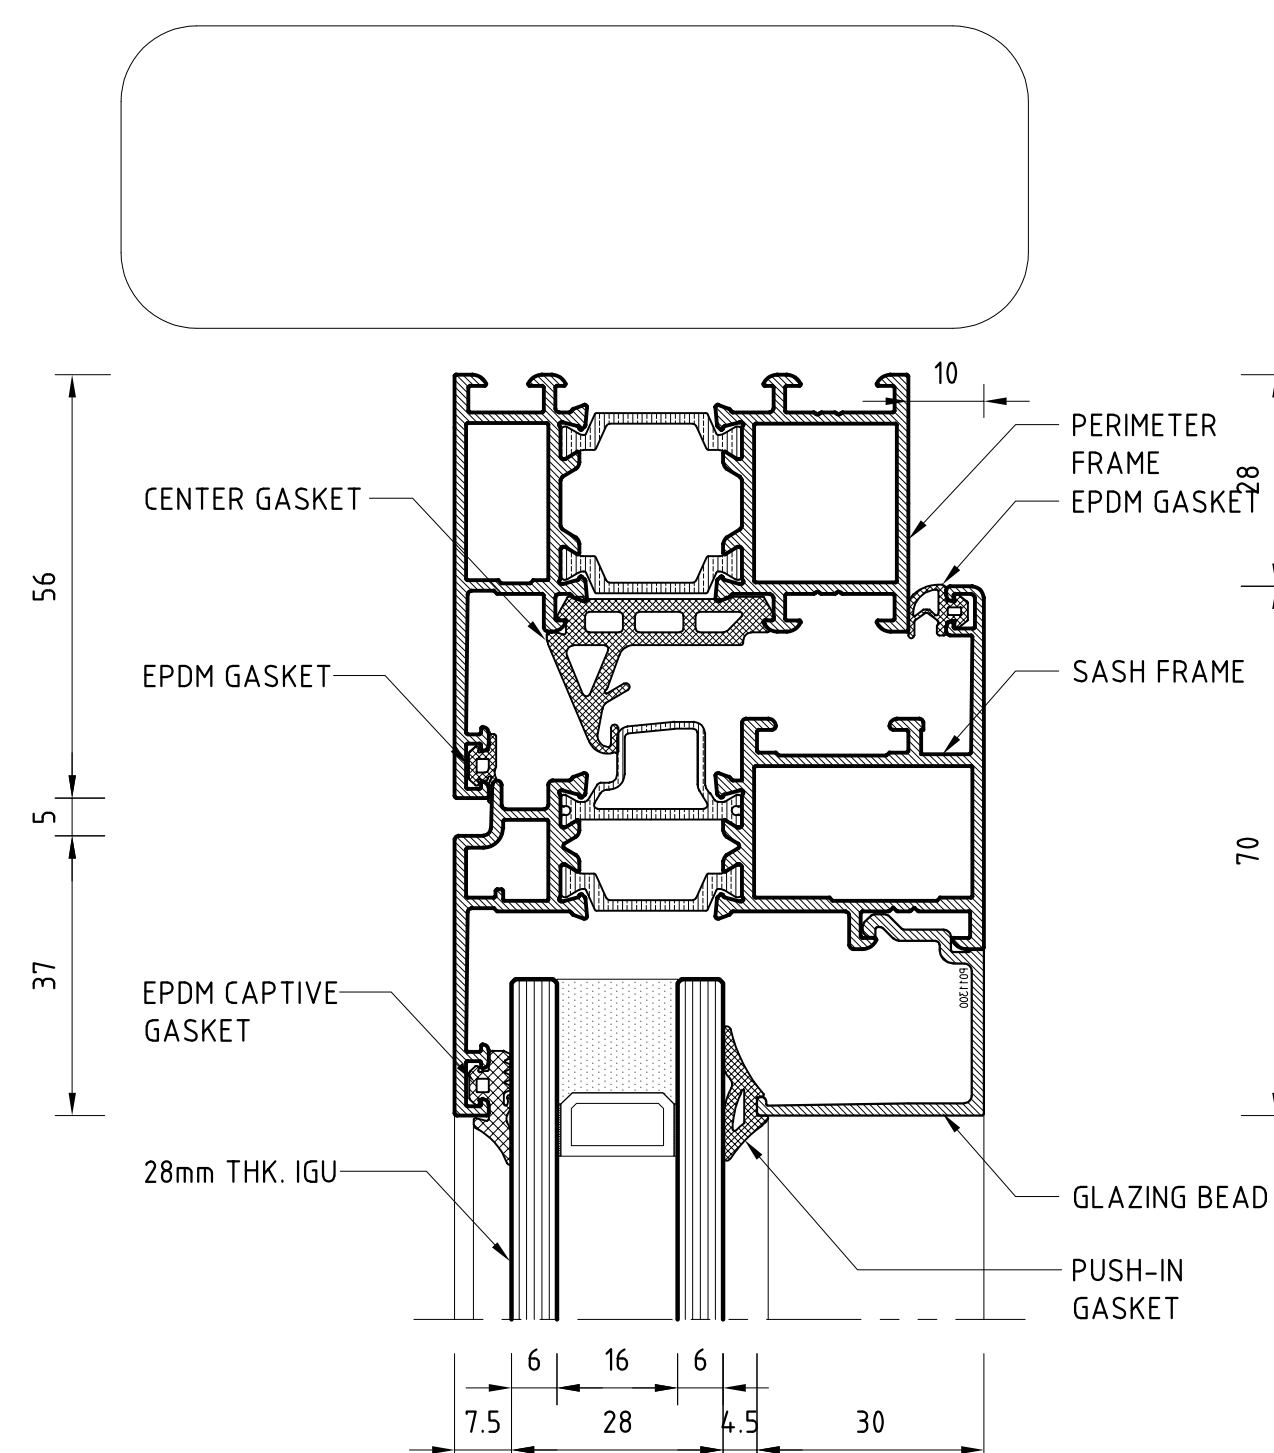

HEAD DETAIL

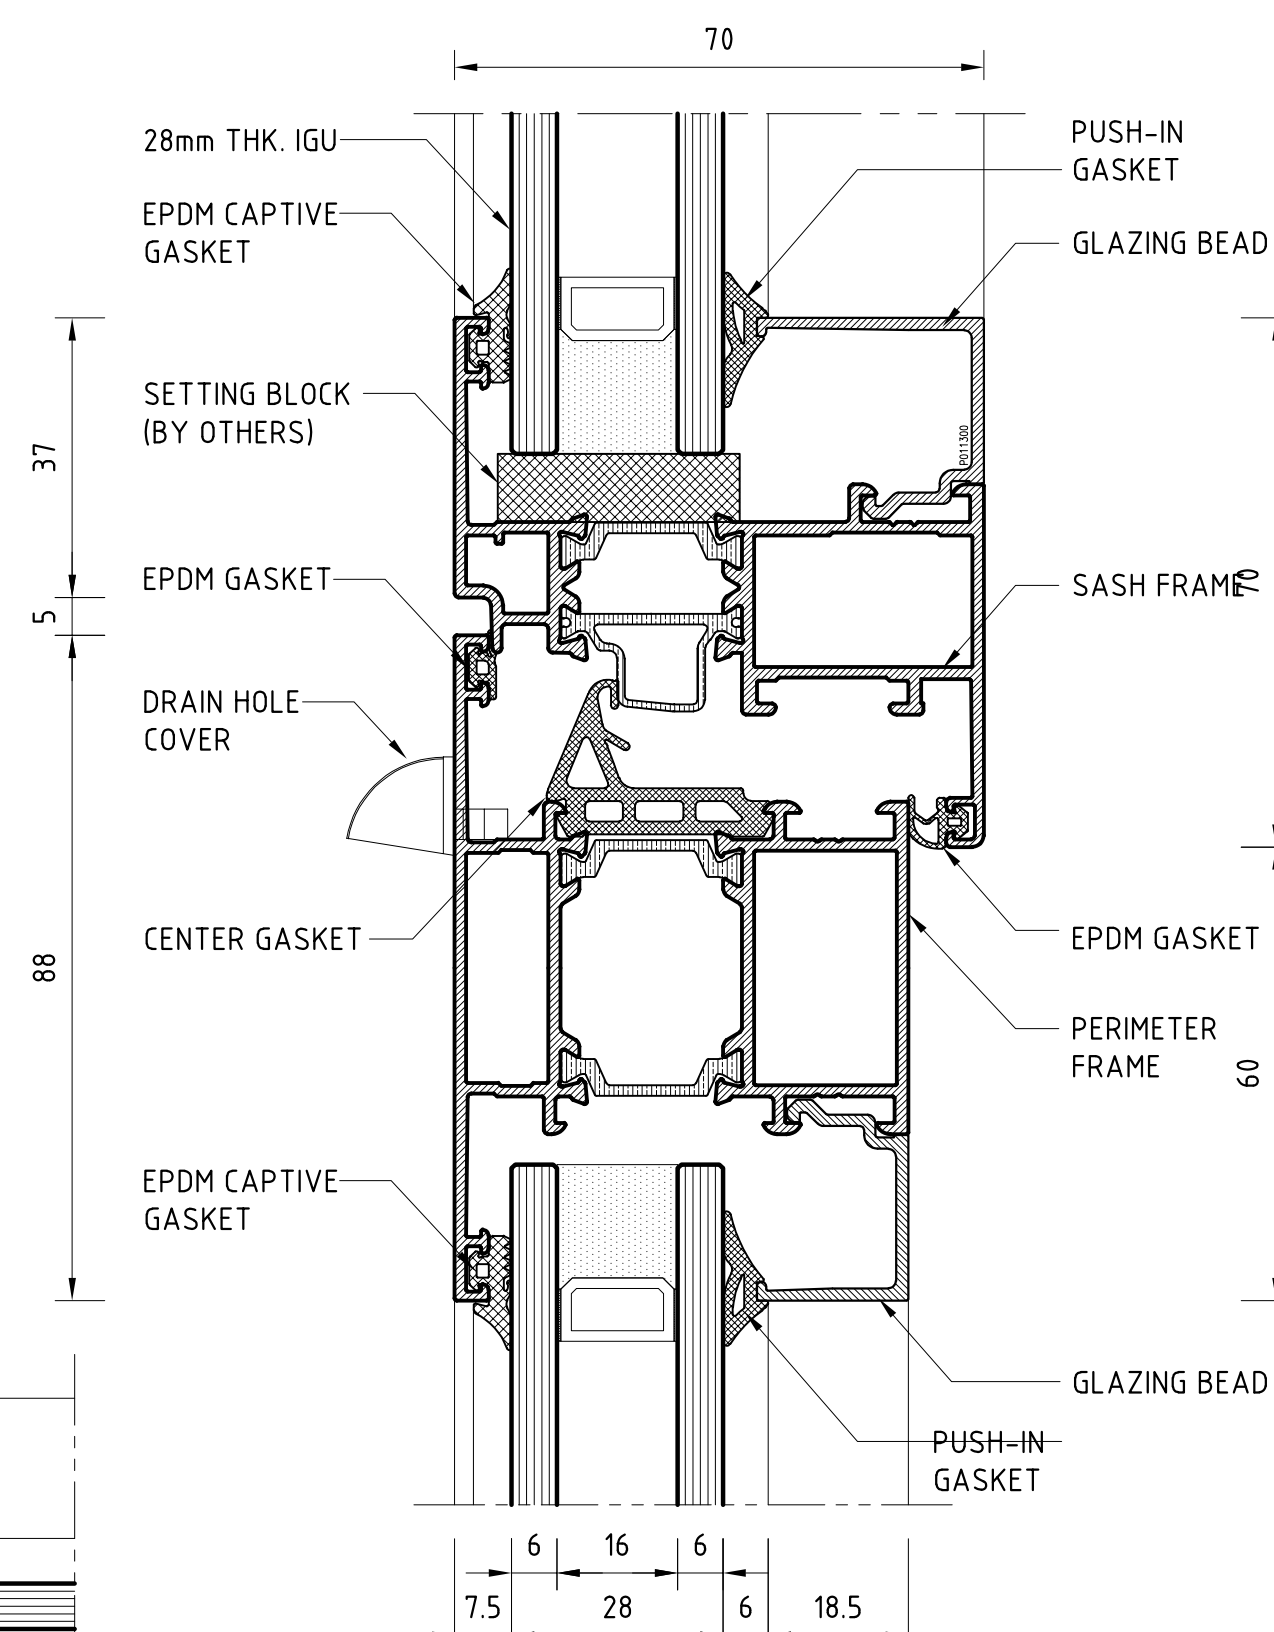

HORIZONTAL FRAME DETAIL

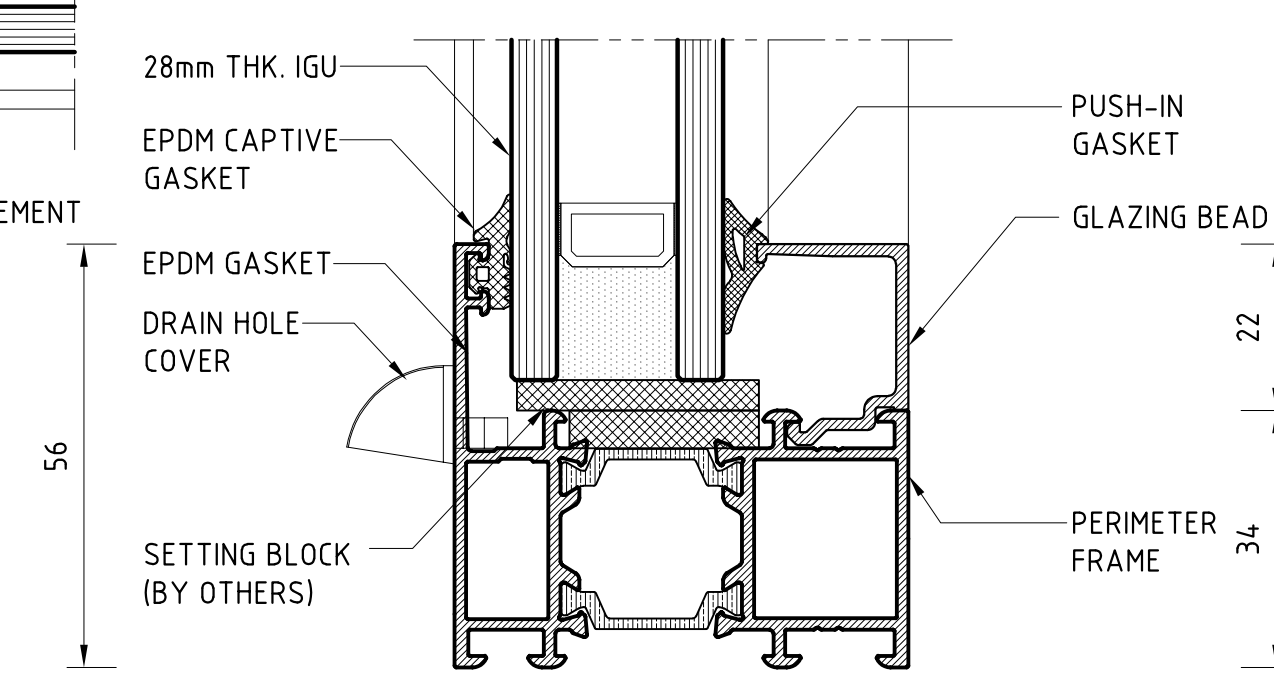

SILL DETAIL

Project :

AL BANDER DEVELOPMENT RESIDENTIAL BLOCK NO. 6

Consultant :



CID GULF LLC
ENGINEERING COSULTANCY


5th Floor, Super Plaza Building
Box 267, Al-Azaibah North, Muscat, Sultanate of Oman
(P) +968 24507373, (F) + 968 24795958
www.cidgulf.com

Aluminum Fabricator :




MODERN ALUMINUM SERVICES LLC.


P.O.Box 908, P.C.130, Al Azaiba,
Muscat, Sultanate of Oman
TEL: 00968 22826356 / 24446398

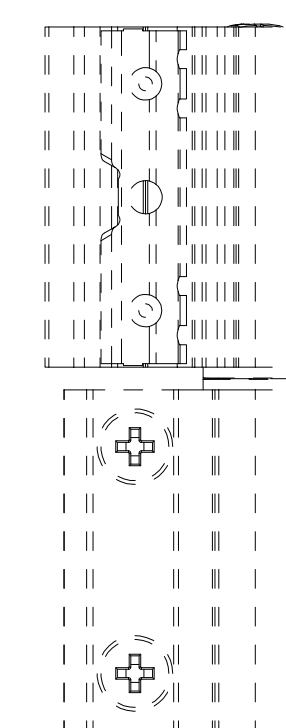


00136
FLUSH BASE HINGES

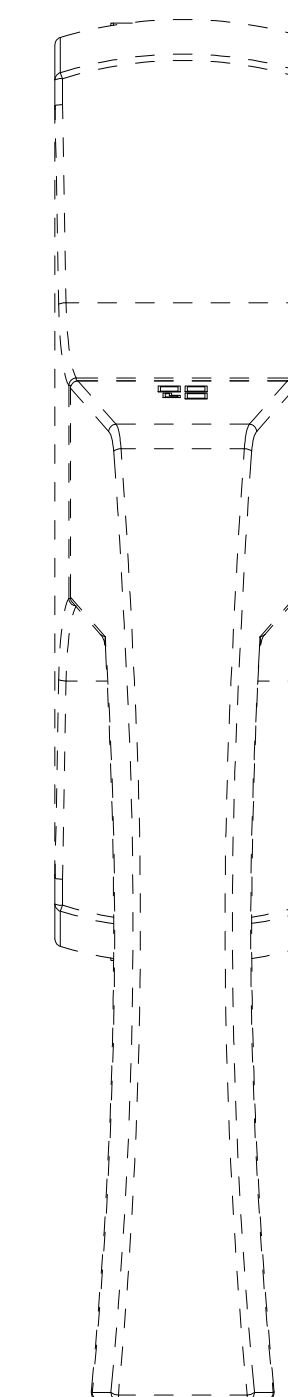

01076
CREMONE HANDLE

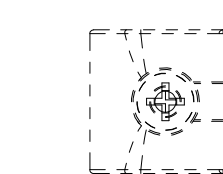


02352
WING LIFT PLATE

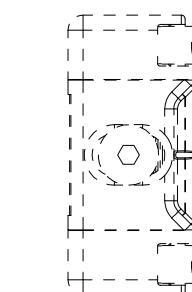


01347
ADJUSTABLE STRIKER




04027
FIXED PAWL

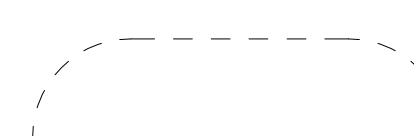


2145
DRAIN COVER w/ VALVE

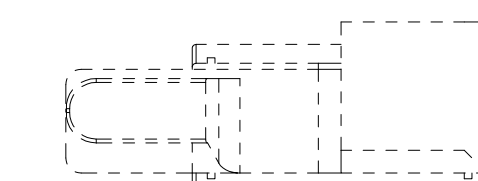


02387K
CONNECTOR BLOCK

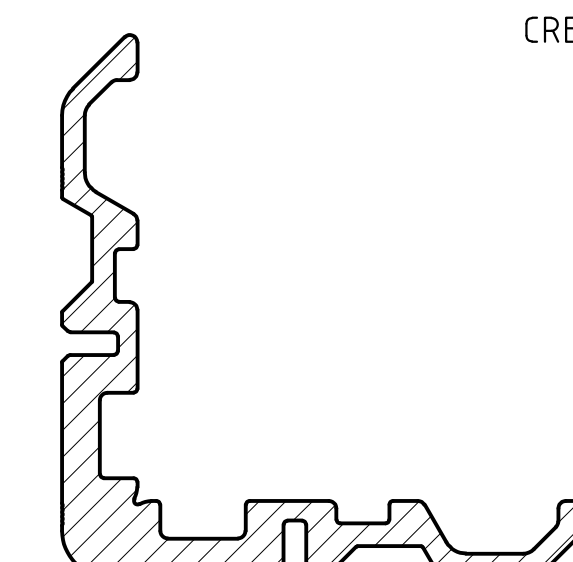


P010100
CORNER CLEAT 10mm

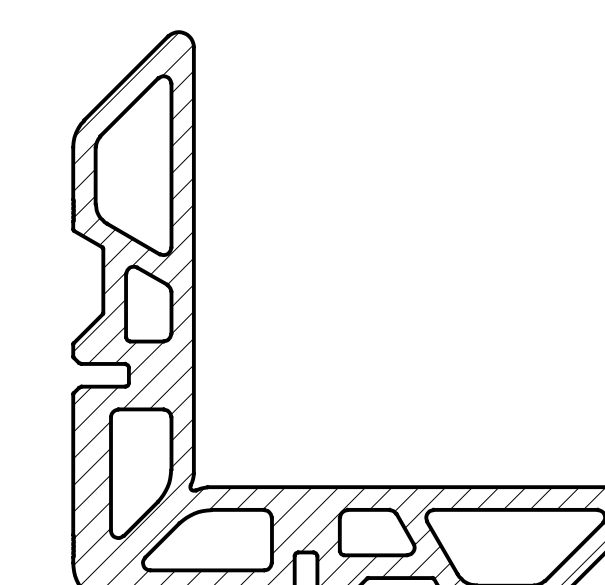


P010160
CORNER CLEAT 16mm

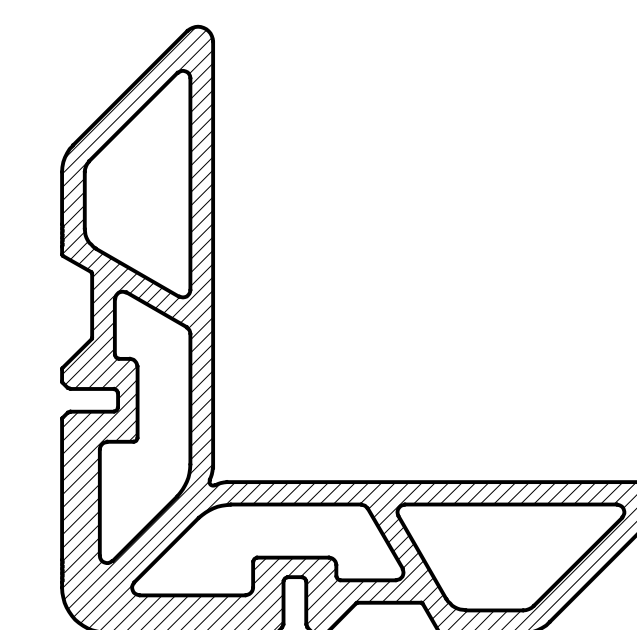

P010200
CORNER CLEAT 20mm

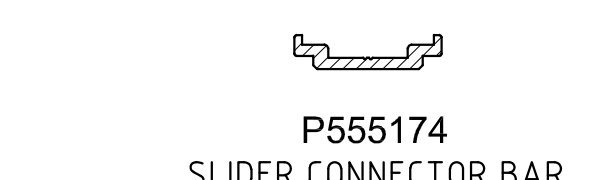


P555174
SLIDER CONNECTOR BAR

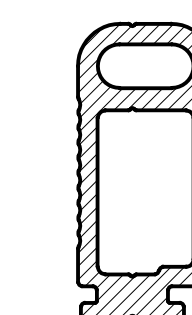


P010900
T-CONNECTOR



P010901
T-CONNECTOR

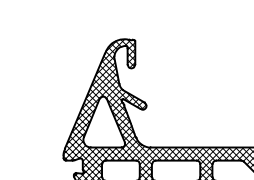

G 1001
CENTRAL GASKET

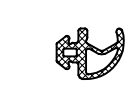


G 1002
SASH GASKET



G 1003
FRAME GASKET



G 1030
GLAZING GASKET GASKET

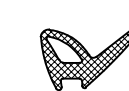

Z-Gasket-01
PUSH-IN GASKET