
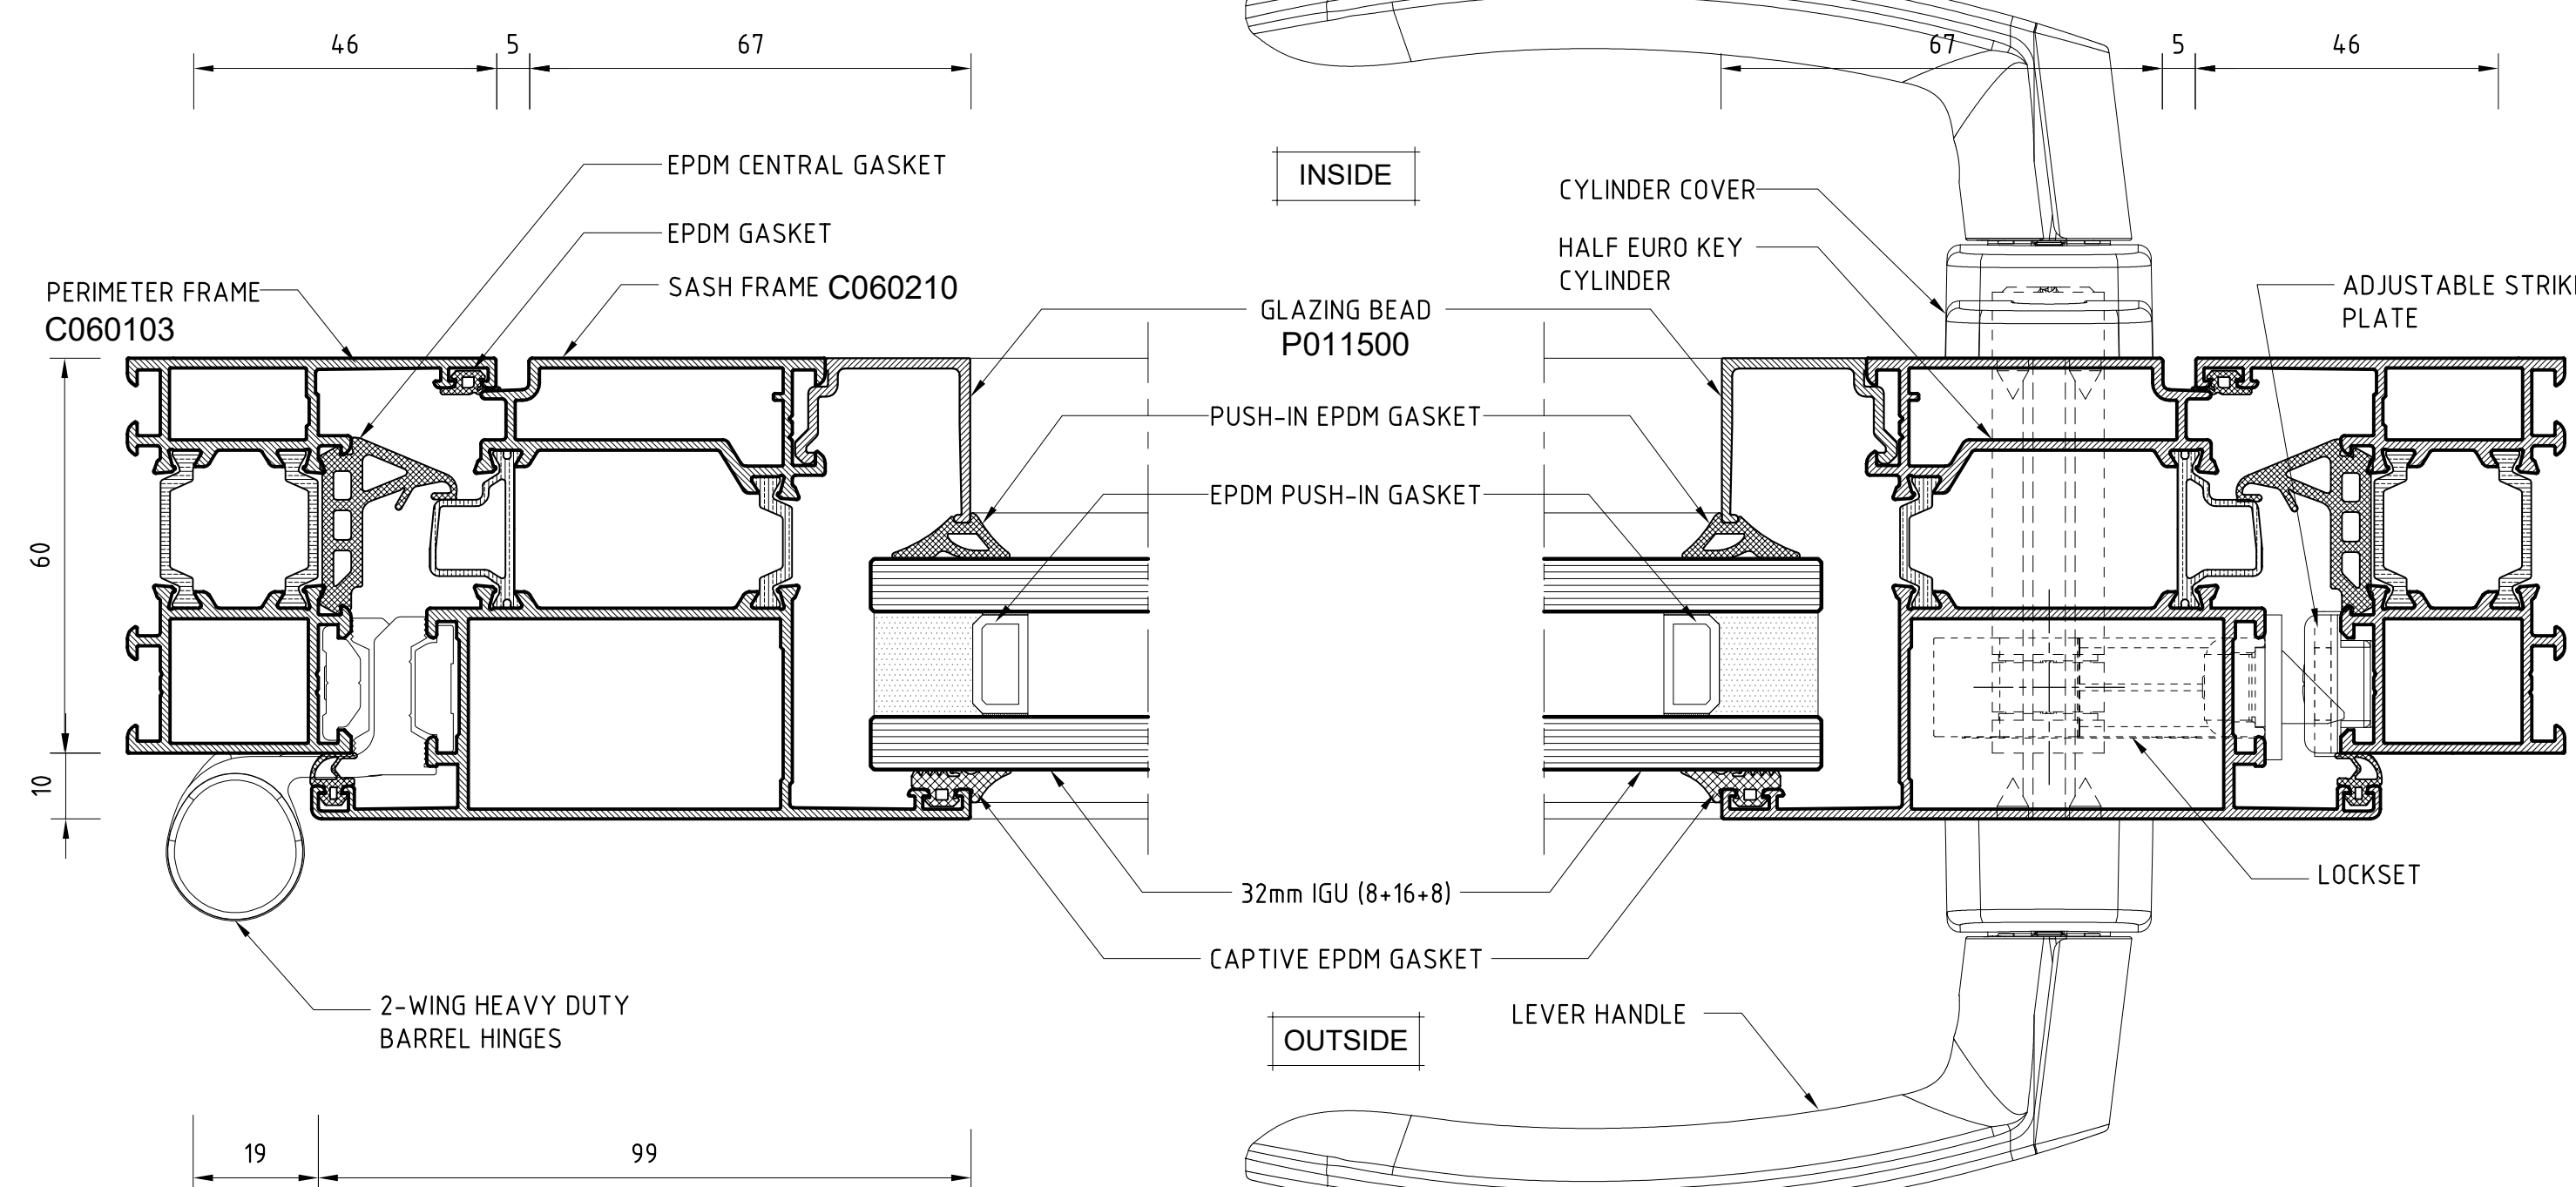
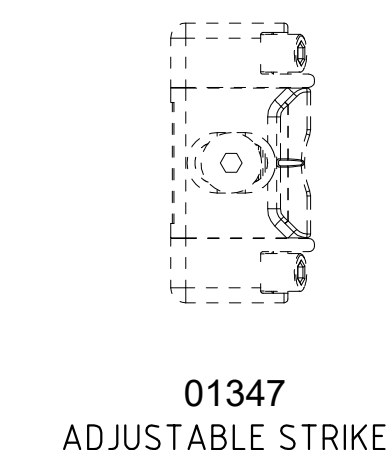
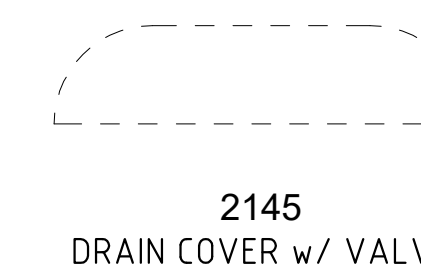
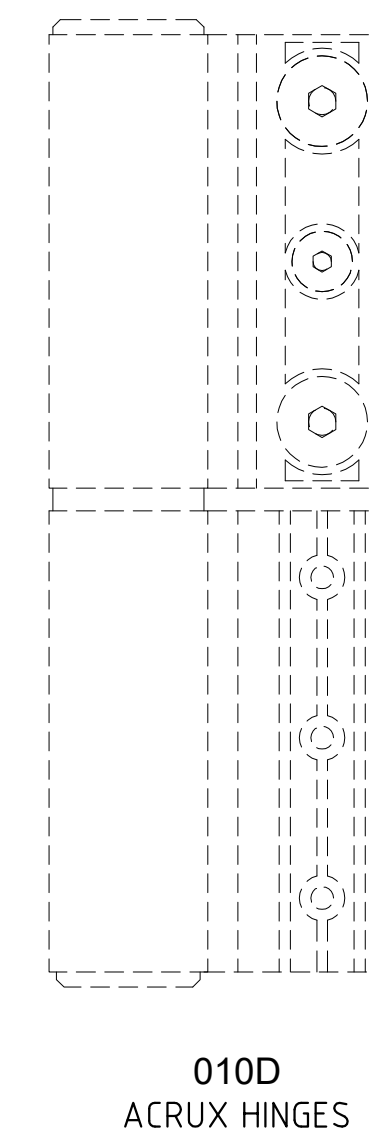
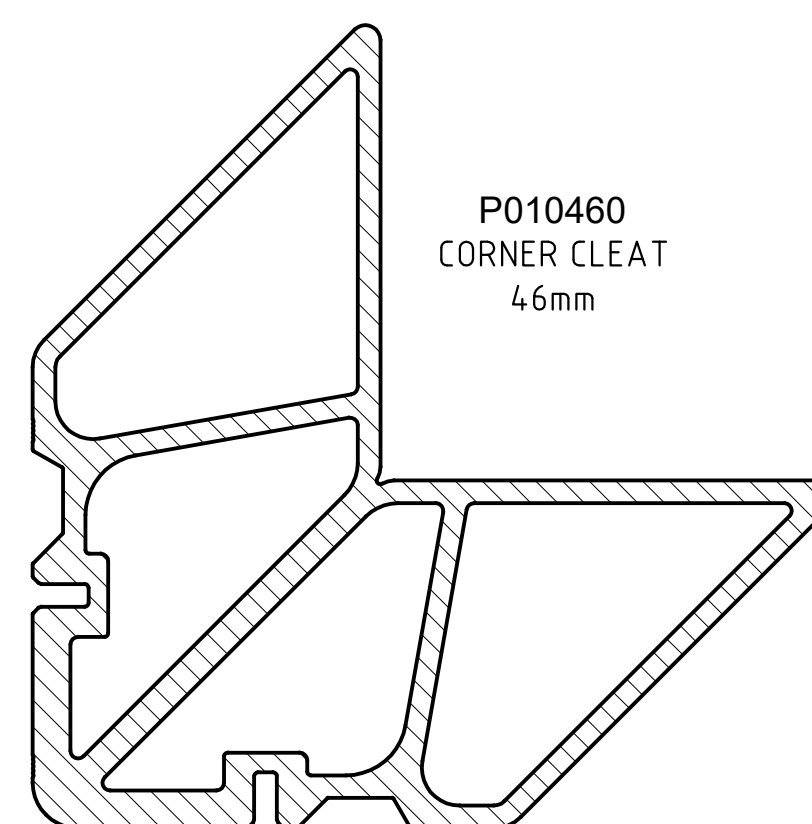
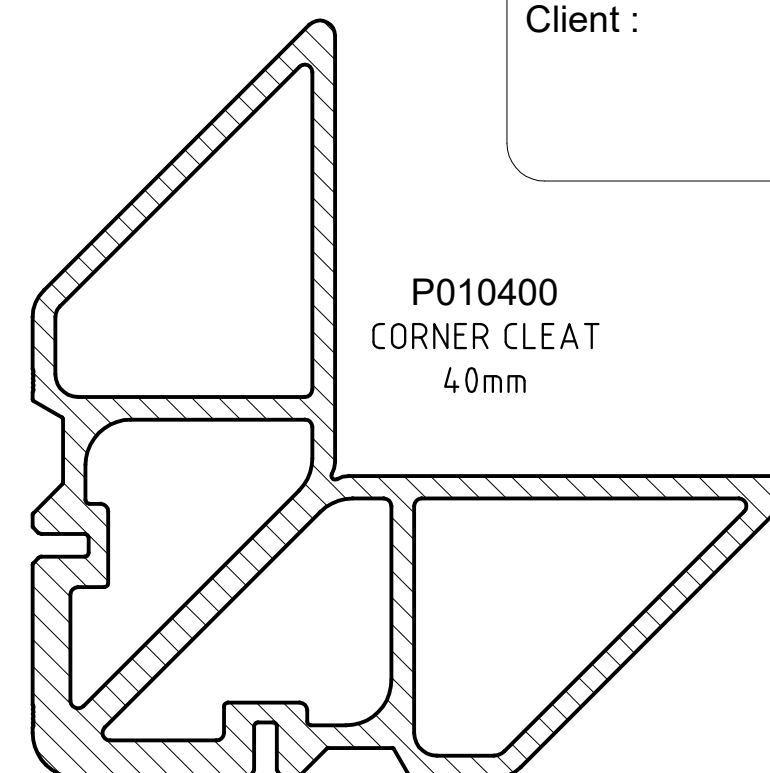
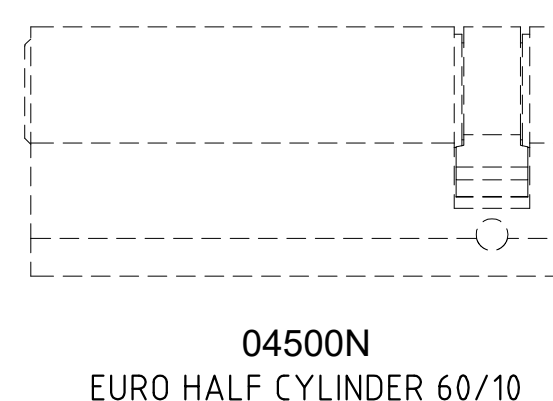
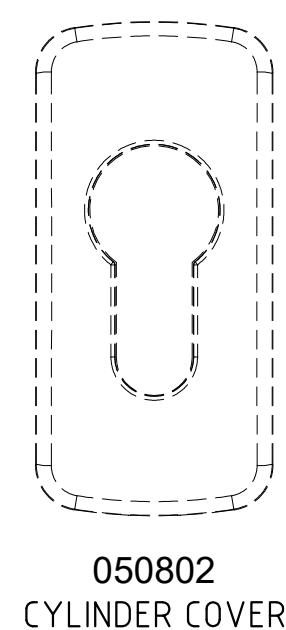
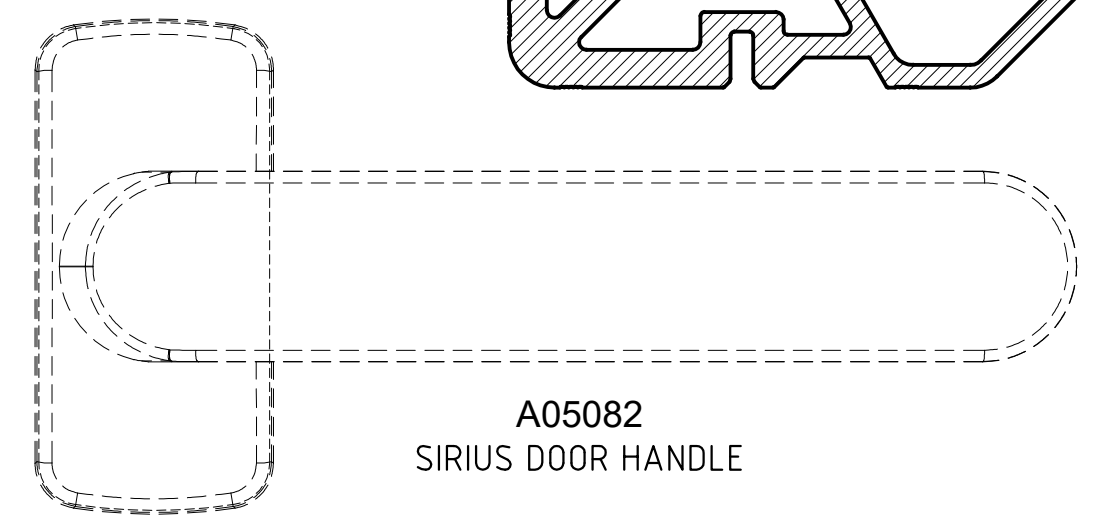
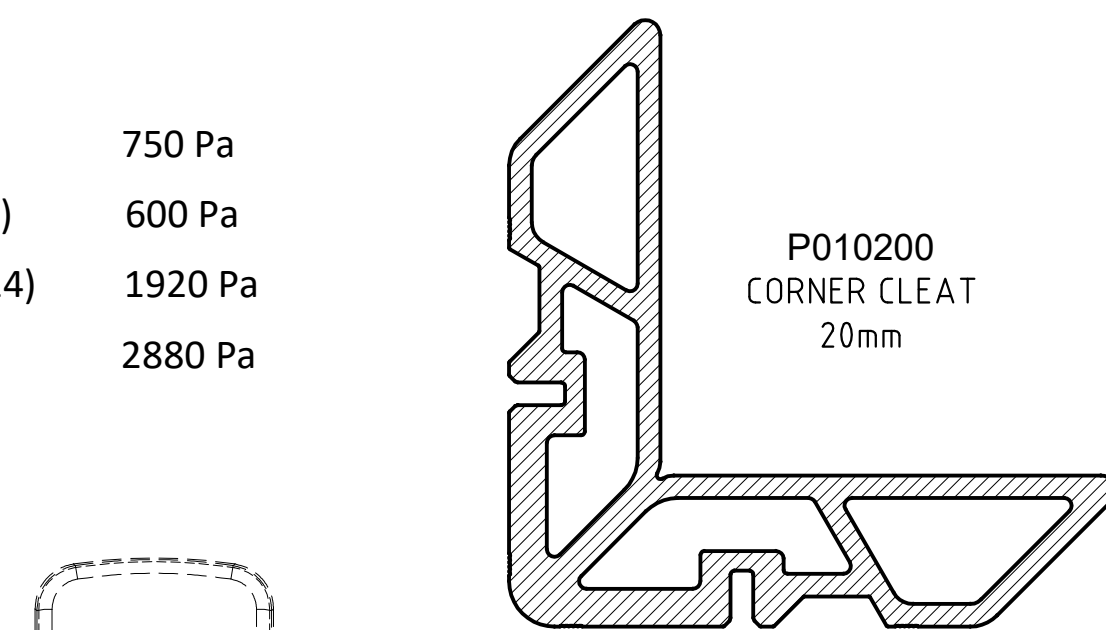
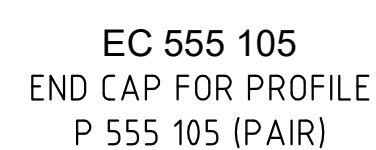
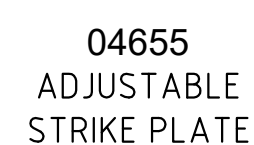
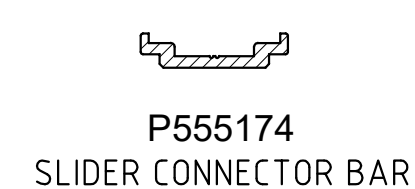
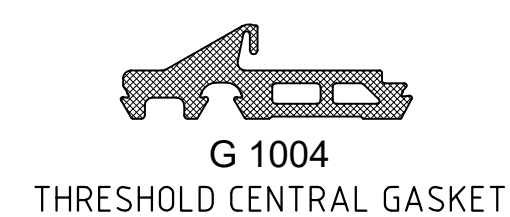
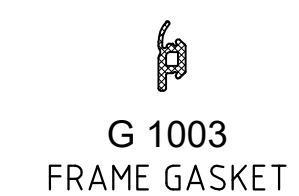


S 60


Swing-Out Hinged Door System

CERTIFICATIONS


- Air infiltration & Exfiltration (ASTM E283/E283M-19) 750 Pa
- Water Penetration (ASTM E331-00 Reapproved 2016) 600 Pa
- Wind Resistance Serviceability (ASTM E330/E330M-14) 1920 Pa
- Wind Resistance Safety (ASTM E330/E330M-14) 2880 Pa

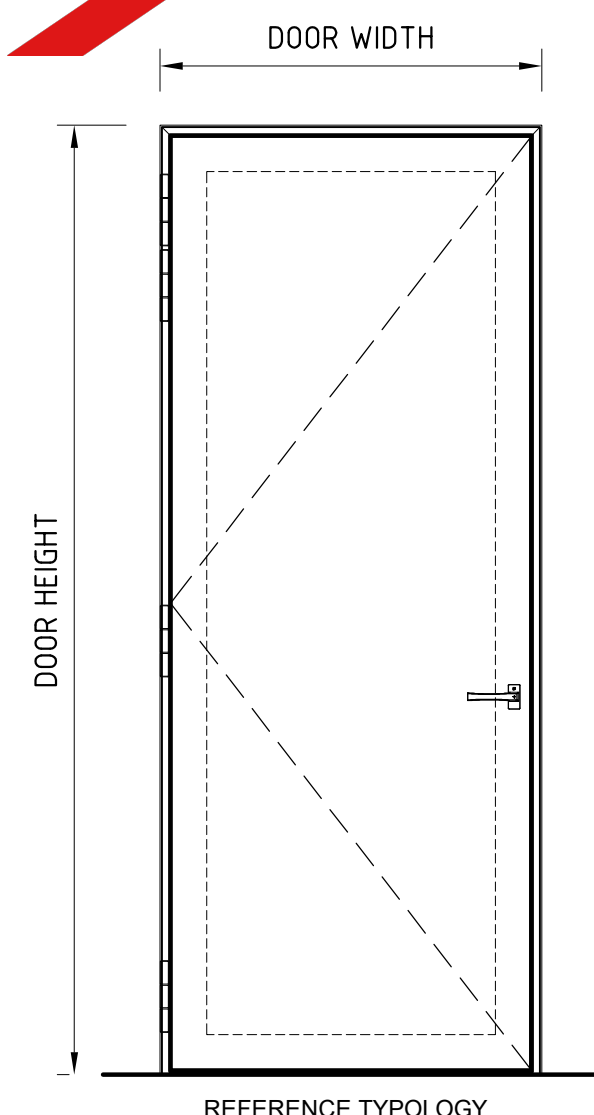

JAMB DETAILS

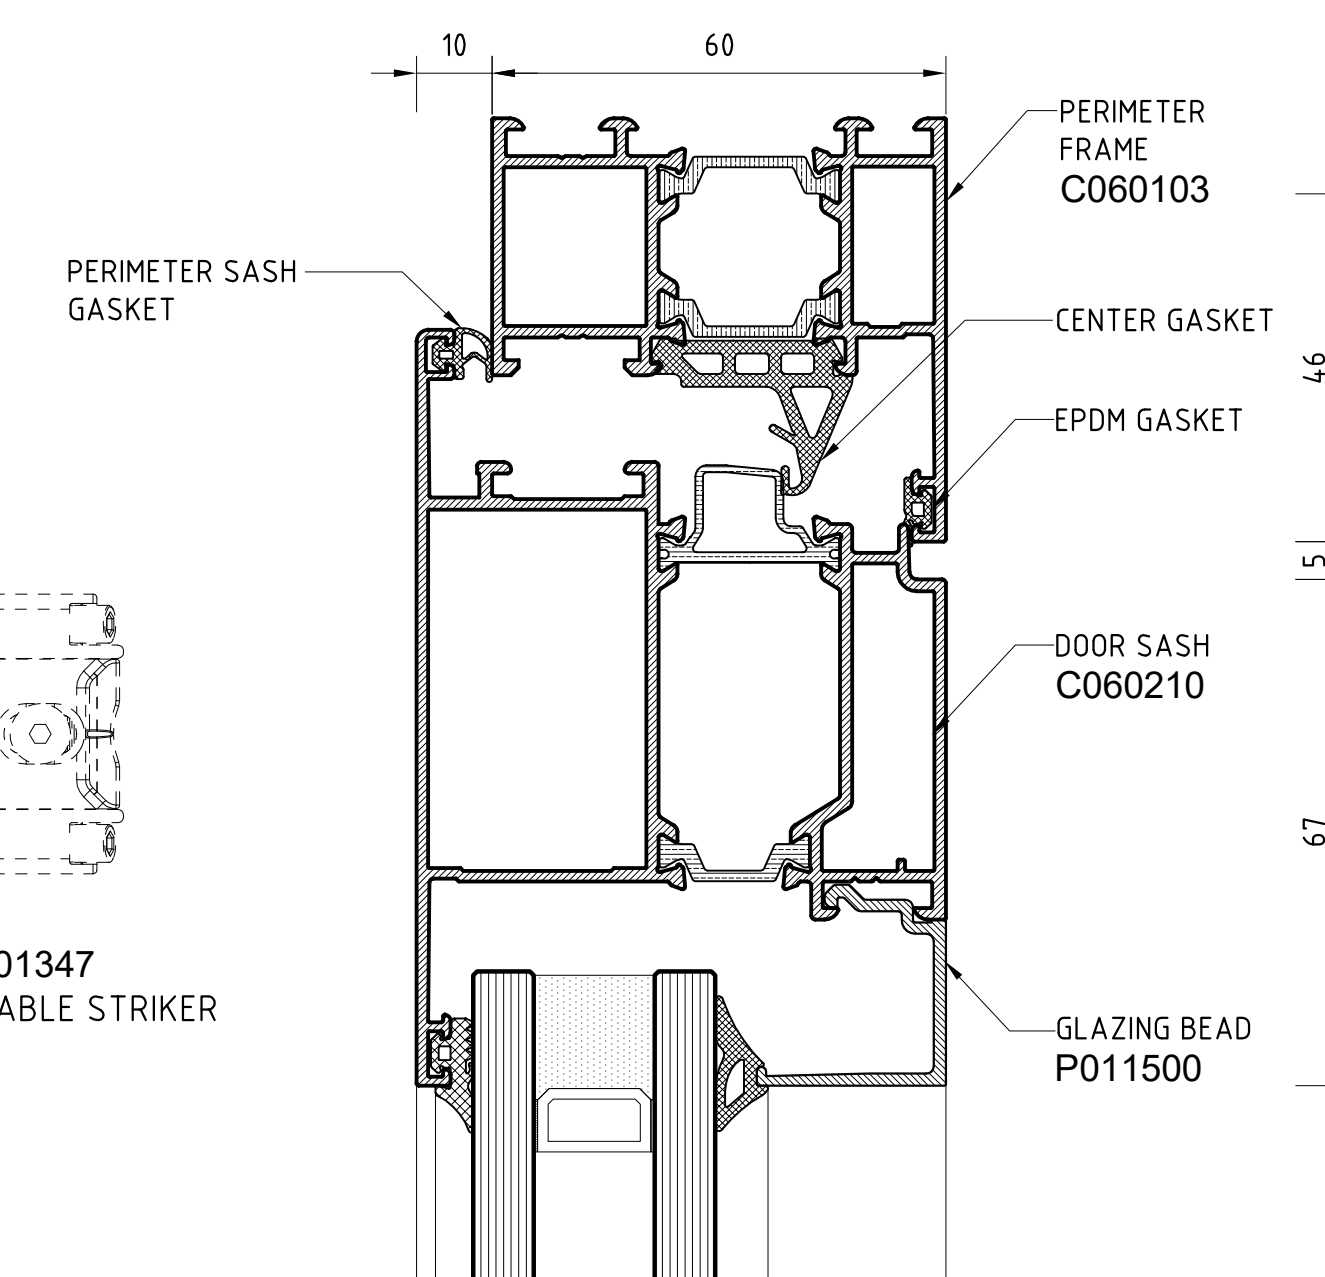

HEAD DETAIL

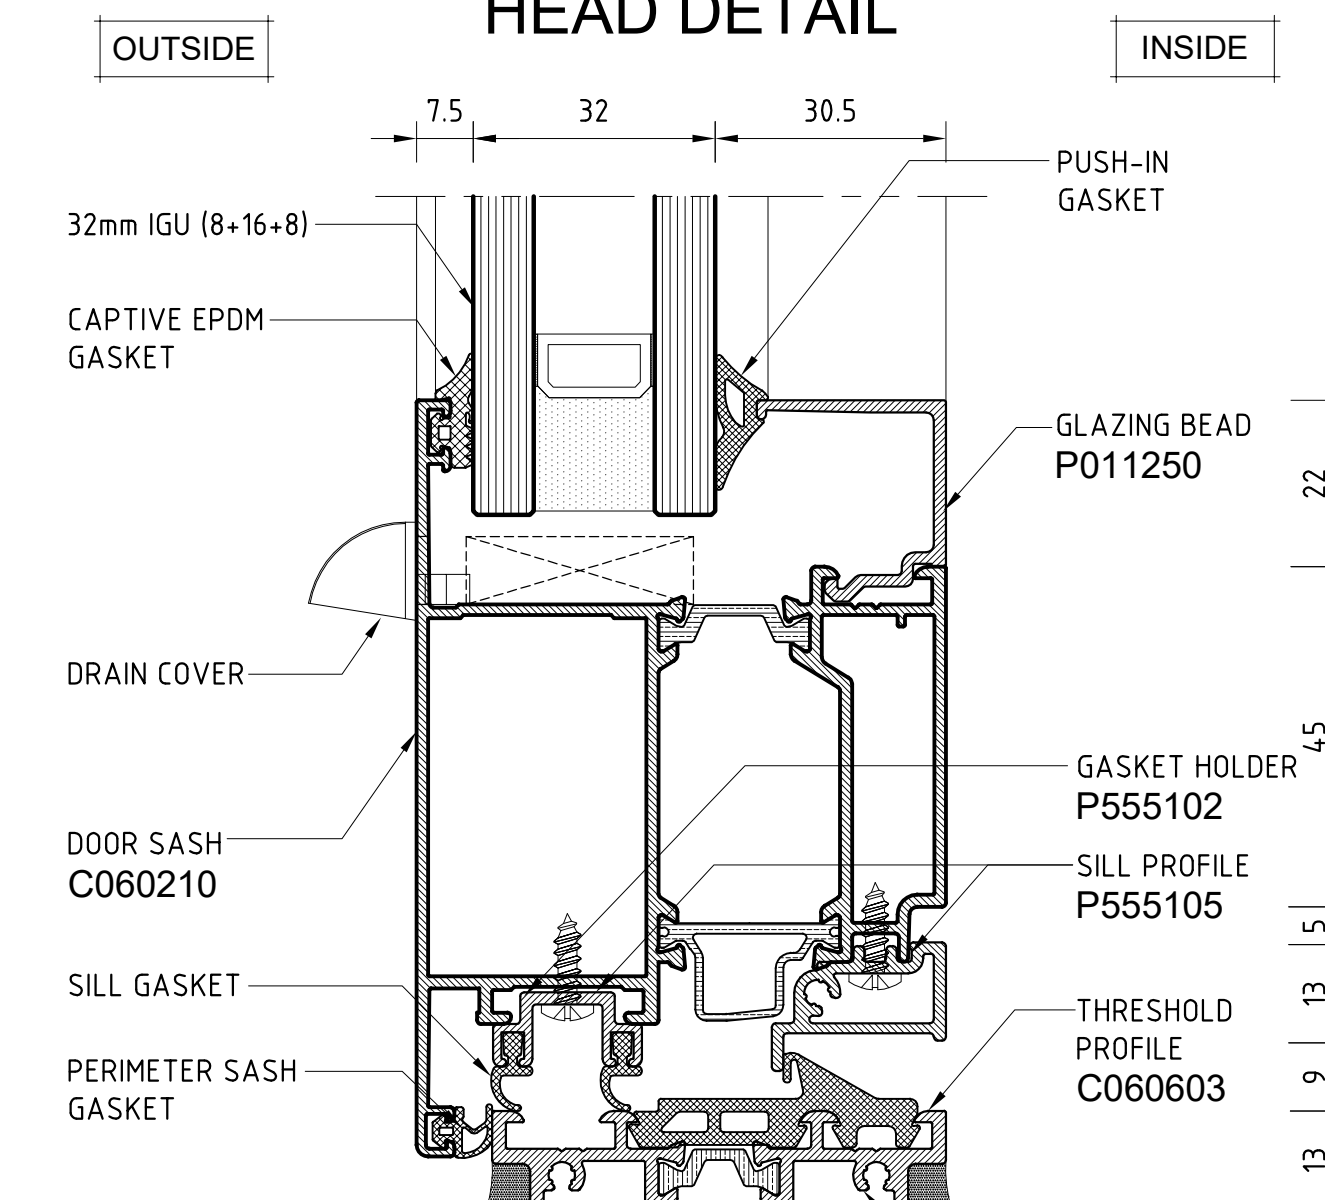

SILL DETAIL

Project : AJMAN CREEK TOWERS , Rashidia 01, Ajman U.A.E.

Consultant :



Client :

Mr. Ghaleb Kamel Jaber

support@sykon.ae
www.sykon.ae

