




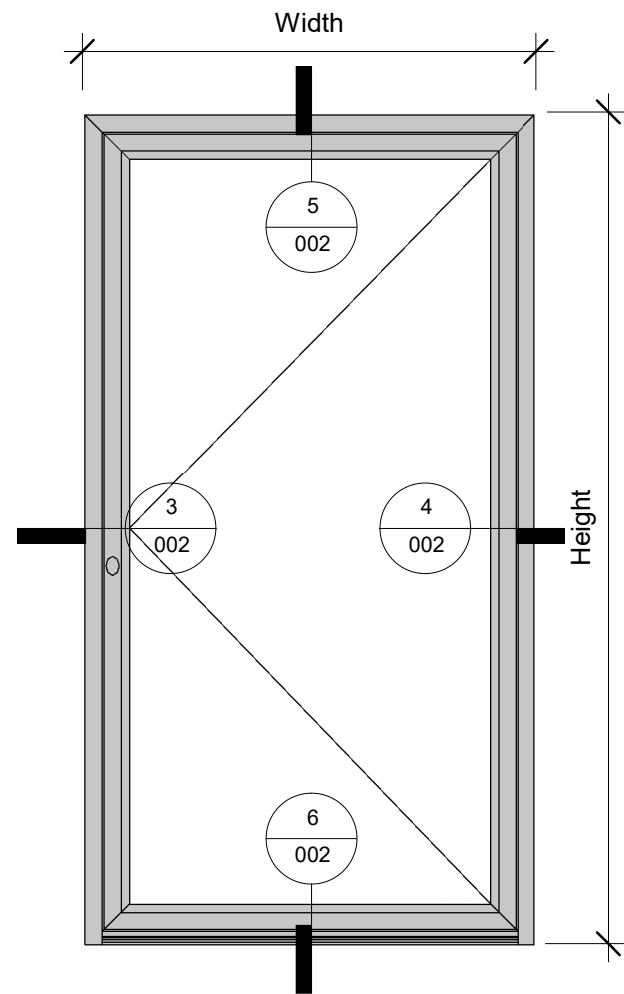


1 Elevation Front
1 : 20

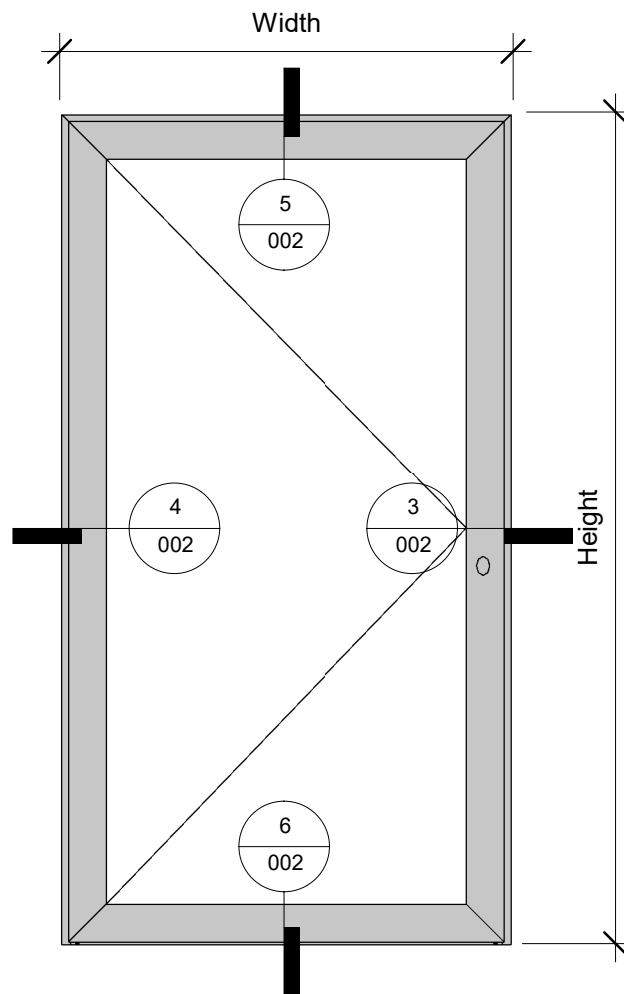


2 Elevation Back
1 : 20

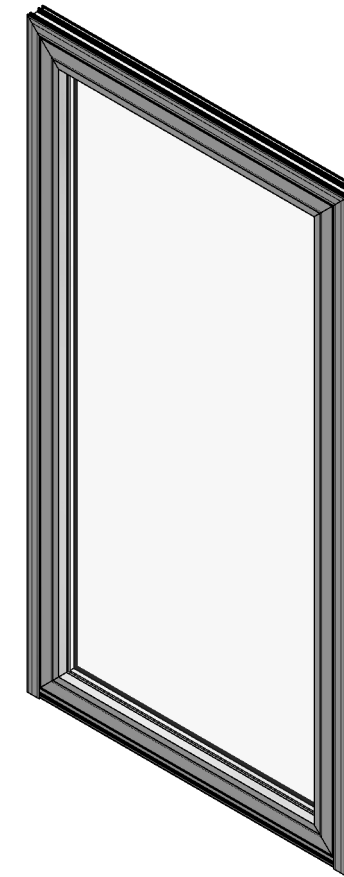


7 3D View

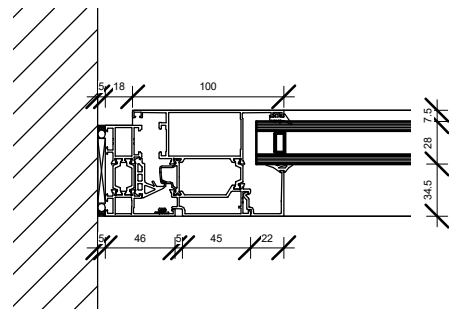


3 Detail 1
1 : 5

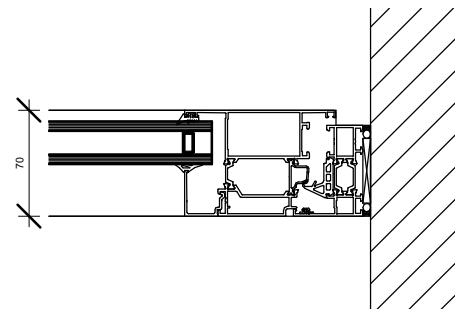

4 Detail 2
1 : 5

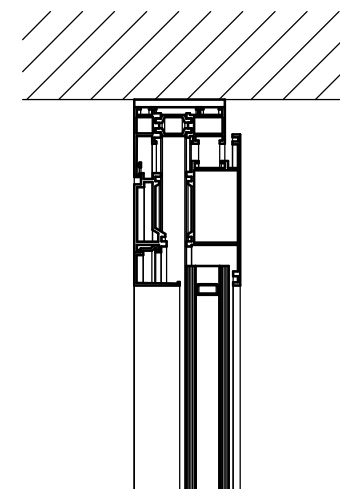

5 Detail 3
1 : 5

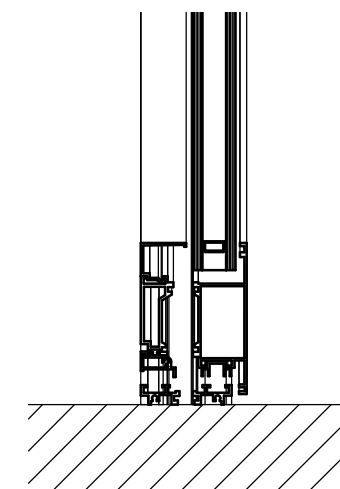

6 Detail 4
1 : 5

NOTE:
* All dimensions are in mm. unless otherwise specified.

CONSULTANT/CLIENT APPROVAL			
No.	STATUS	DATE	
A	APPROVED		
B	APPROVED AS NOTED		
C	NOT APPROVED, RESUBMIT		
D	INCOMPLETE, RESUBMIT		
REV.	DESCRIPTION	CHKD	DATE
00	Revision 00		10/09/2024
01	Revision 01		05/11/2024

PROJECT PICTURE:

PROJECT:

CONSULTANT:

CLIENT:

DRAWING CONTENT:

S60 Single Hinged Door
Open Out

DRAWN: SJ	DATE: 05.11.2024	SYSTEM S60
CHECKED: MK	SCALE: As indicated	
DRAWING No. 002		REV. No. 01