

NOTE:
* All dimensions are in mm. unless otherwise specified.

CONSULTANT/CLIENT APPROVAL

No.	STATUS		DATE
A	APPROVED		
B	APPROVED AS NOTED		
C	NOT APPROVED, RESUBMIT		
D	INCOMPLETE, RESUBMIT		
REV.	DESCRIPTION	CHKD	DATE
00	Revision 00		10/09/2024
01	Revision 01		05/11/2024

PROJECT PICTURE:

PROJECT:


CONSULTANT:

CLIENT:


DRAWING CONTENT:

SL450


DRAWN: SJ	DATE: 05.11.2024	SYSTEM SL450
CHECKED: MK	SCALE: As indicated	
DRAWING No. 006		REV. No. 01

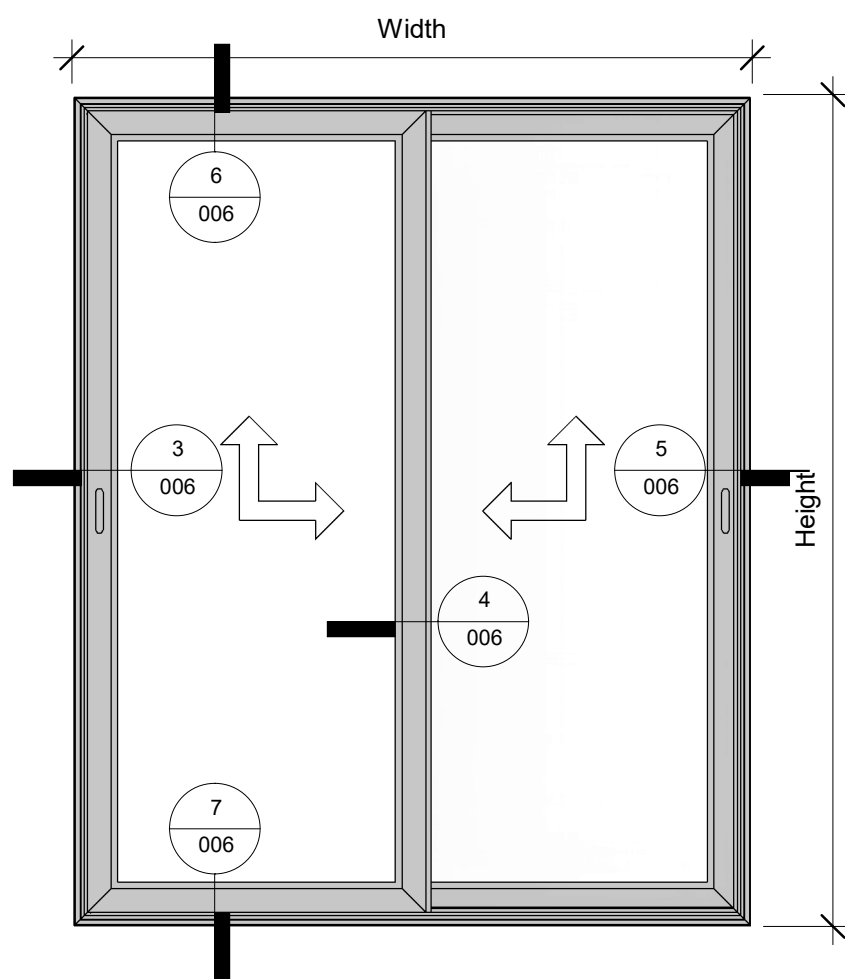


1 Elevation Front
1 : 20

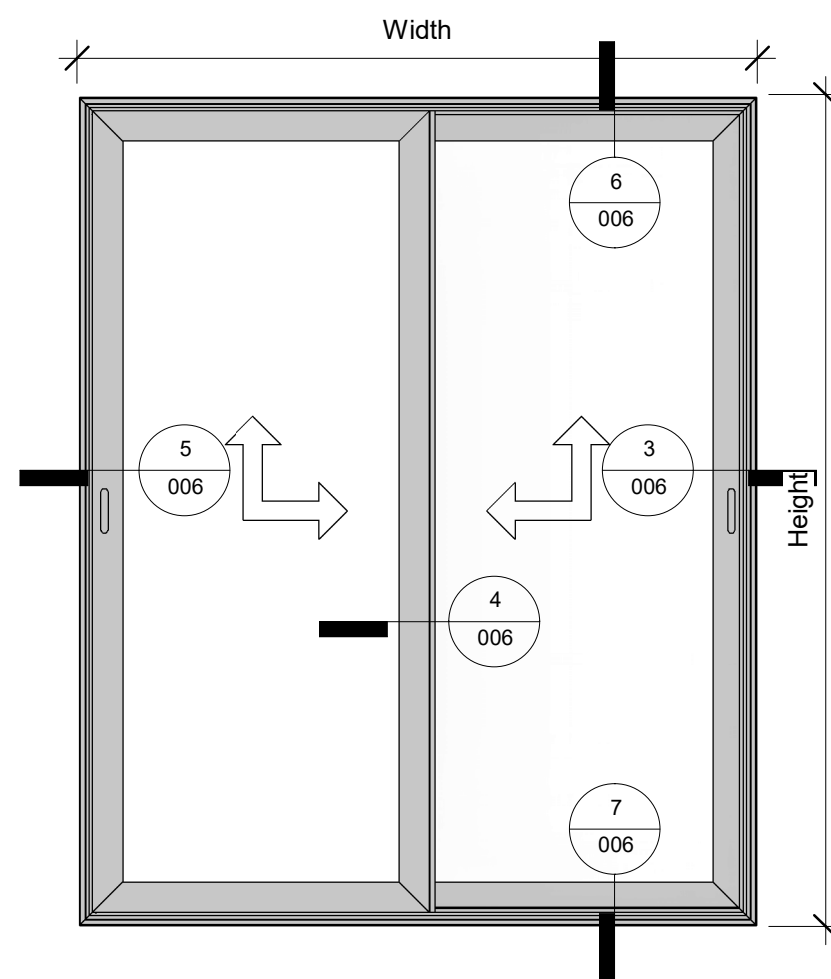

2 Elevation Back
1 : 20

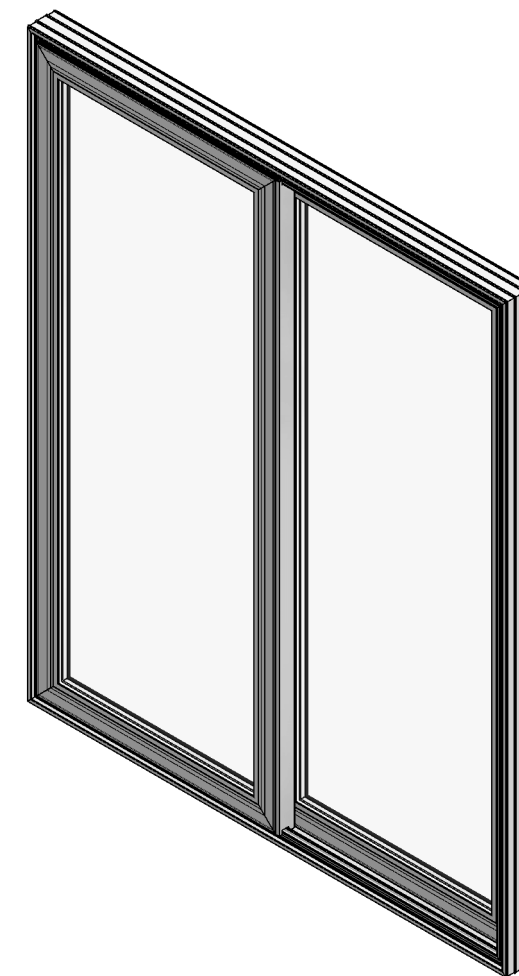


8 3D View

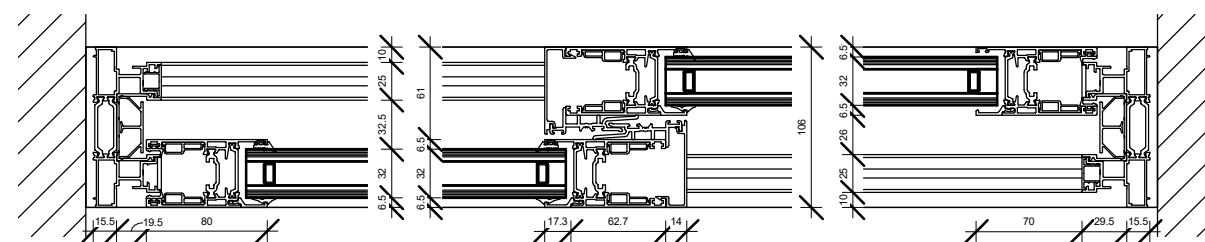


3 Detail 1
1 : 5

4 Detail 2
1 : 5

5 Detail 3
1 : 5

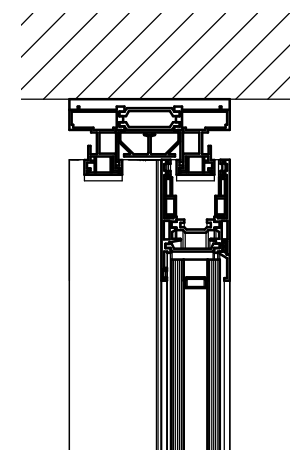

6 Detail 4
1 : 5

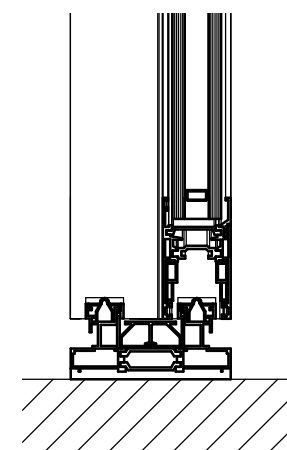

7 Detail 5
1 : 5