



SL 450S

Sliding Door Monorail System

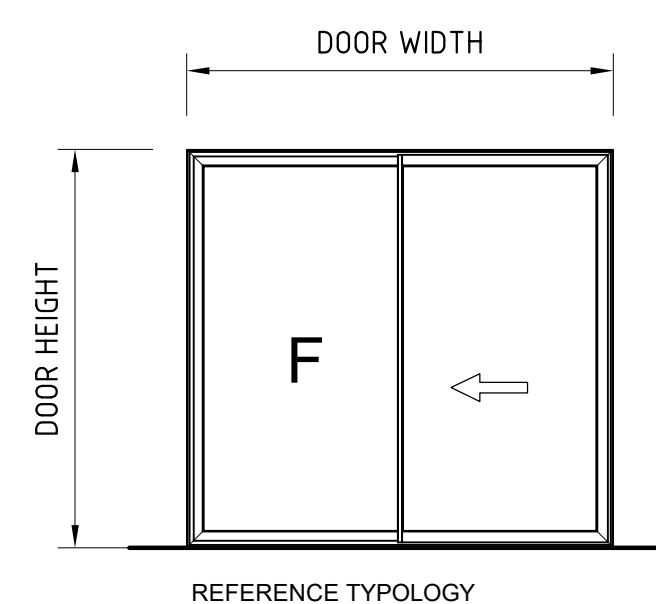

CERTIFICATIONS


- Air Infiltration & Exfiltration (ASTM E283/E283M-19) 600 Pa
- Water Penetration (ASTM E331-00 Reapproved 2016) 600 Pa
- Wind Resistance Serviceability (ASTM E330/E330M-14) 1920 Pa
- Wind Resistance Safety (ASTM E330/E330M-14) 2880 Pa
- Maximum Panel Weight up to 200 kg
- Single Lock Point or Multi-lock points can be used
- Maximum Glass Thickness that can be accommodated is 32mm

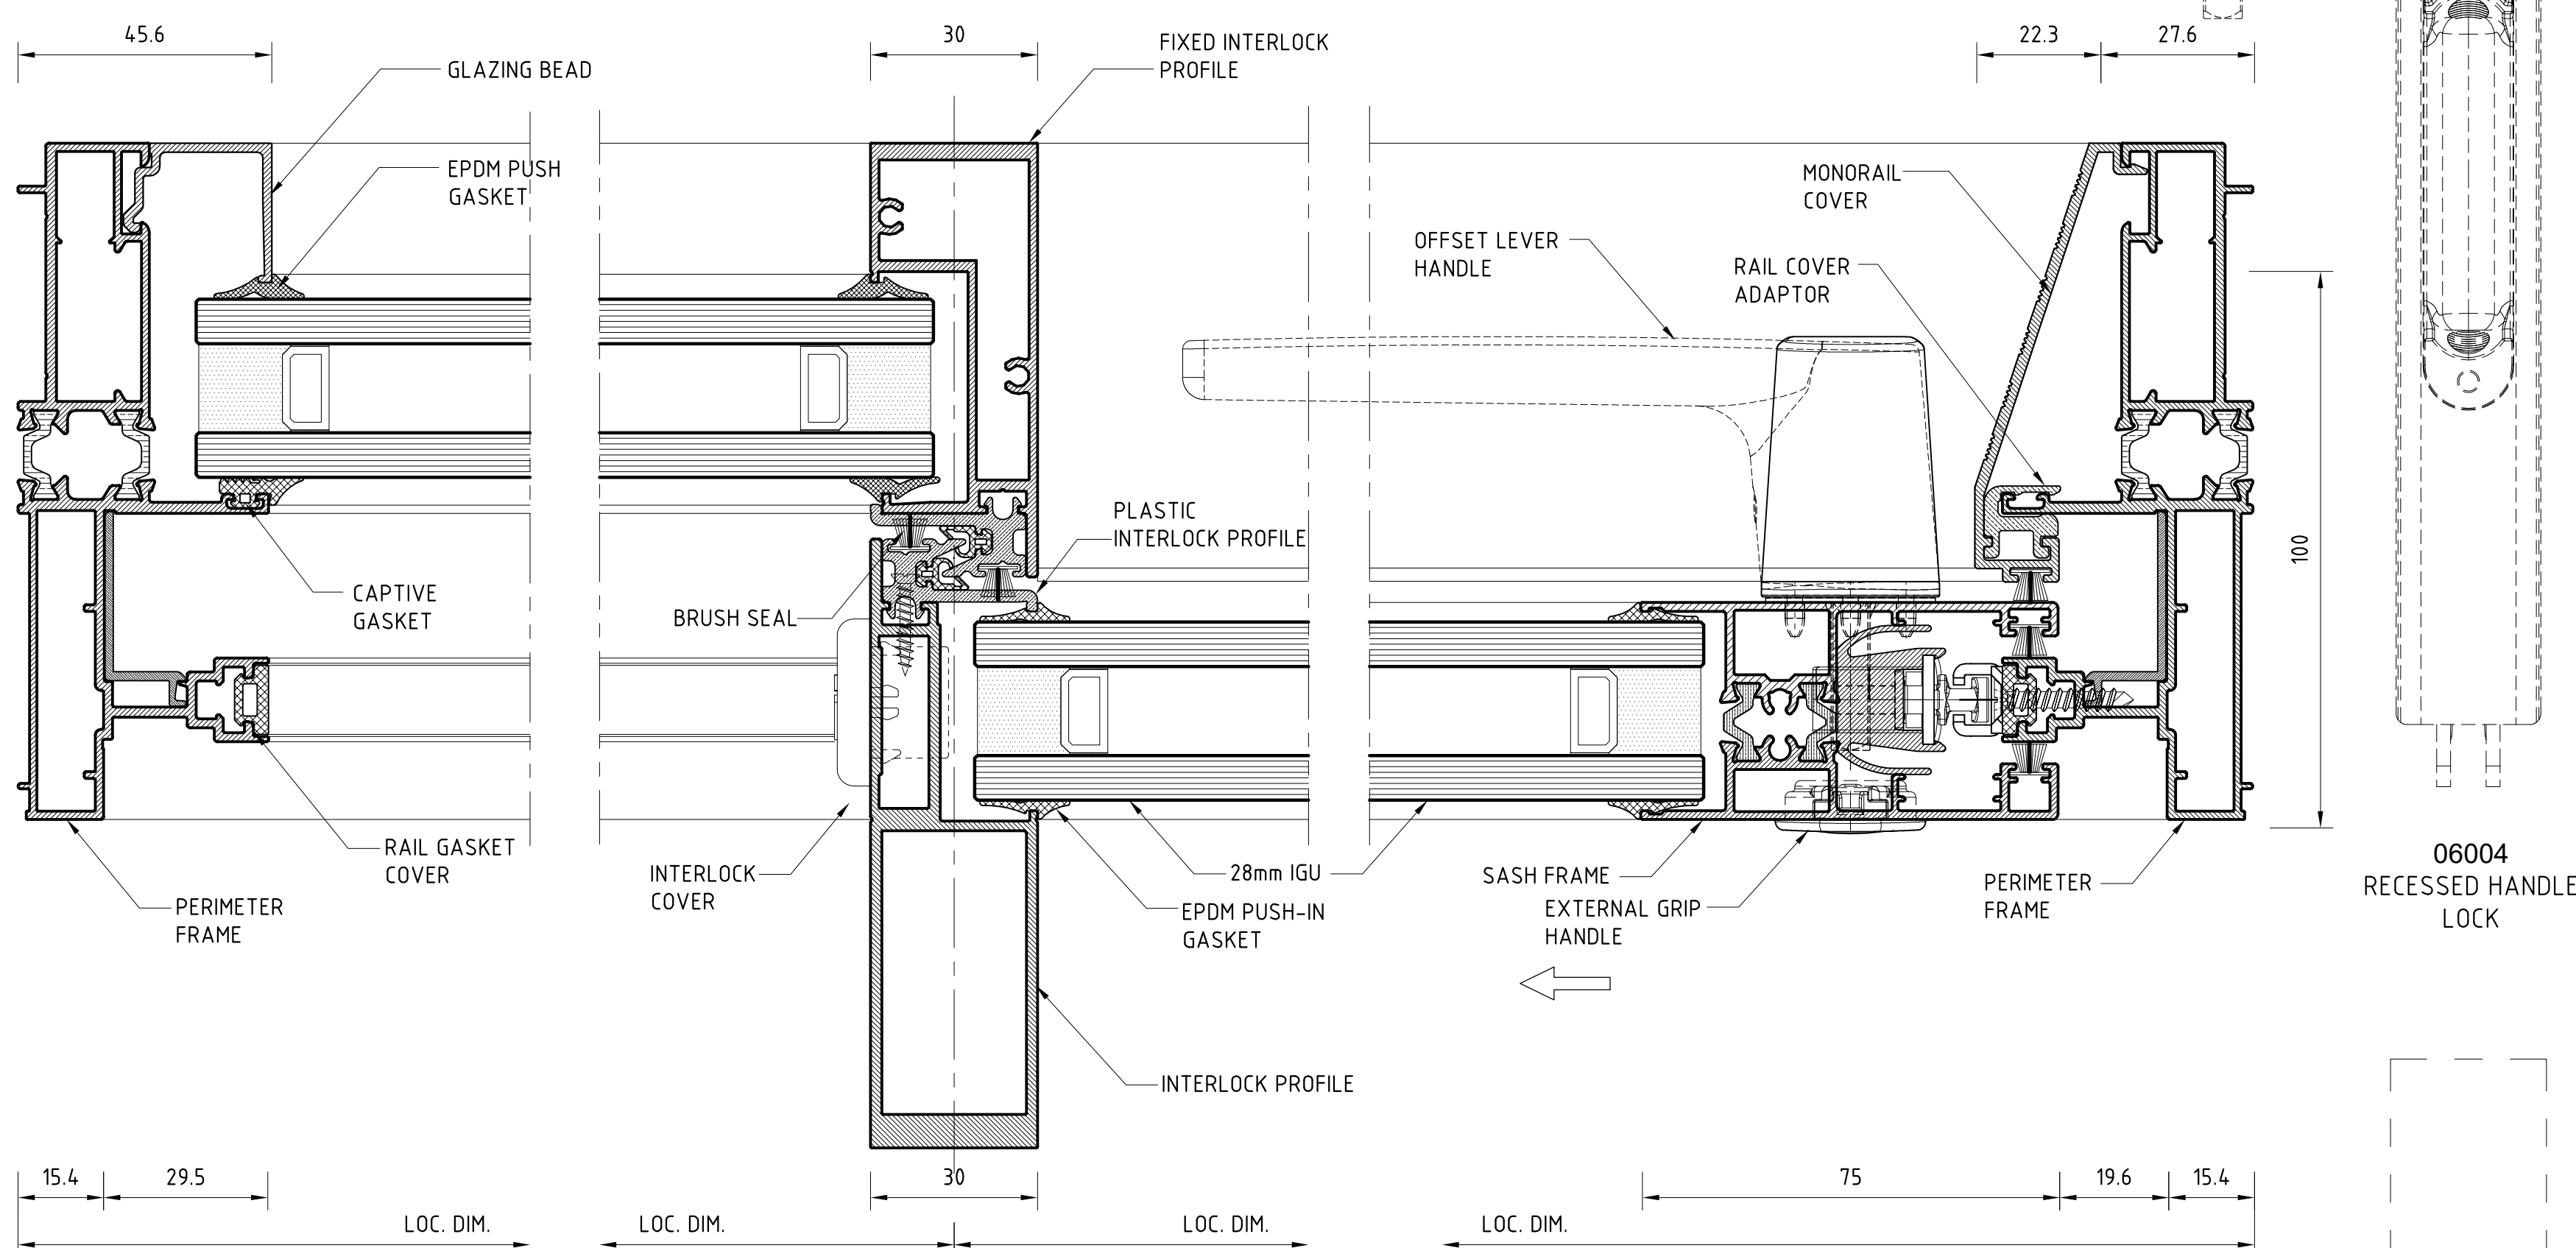

JAMB DETAIL

INTERLOCK DETAIL



JAMB DETAIL

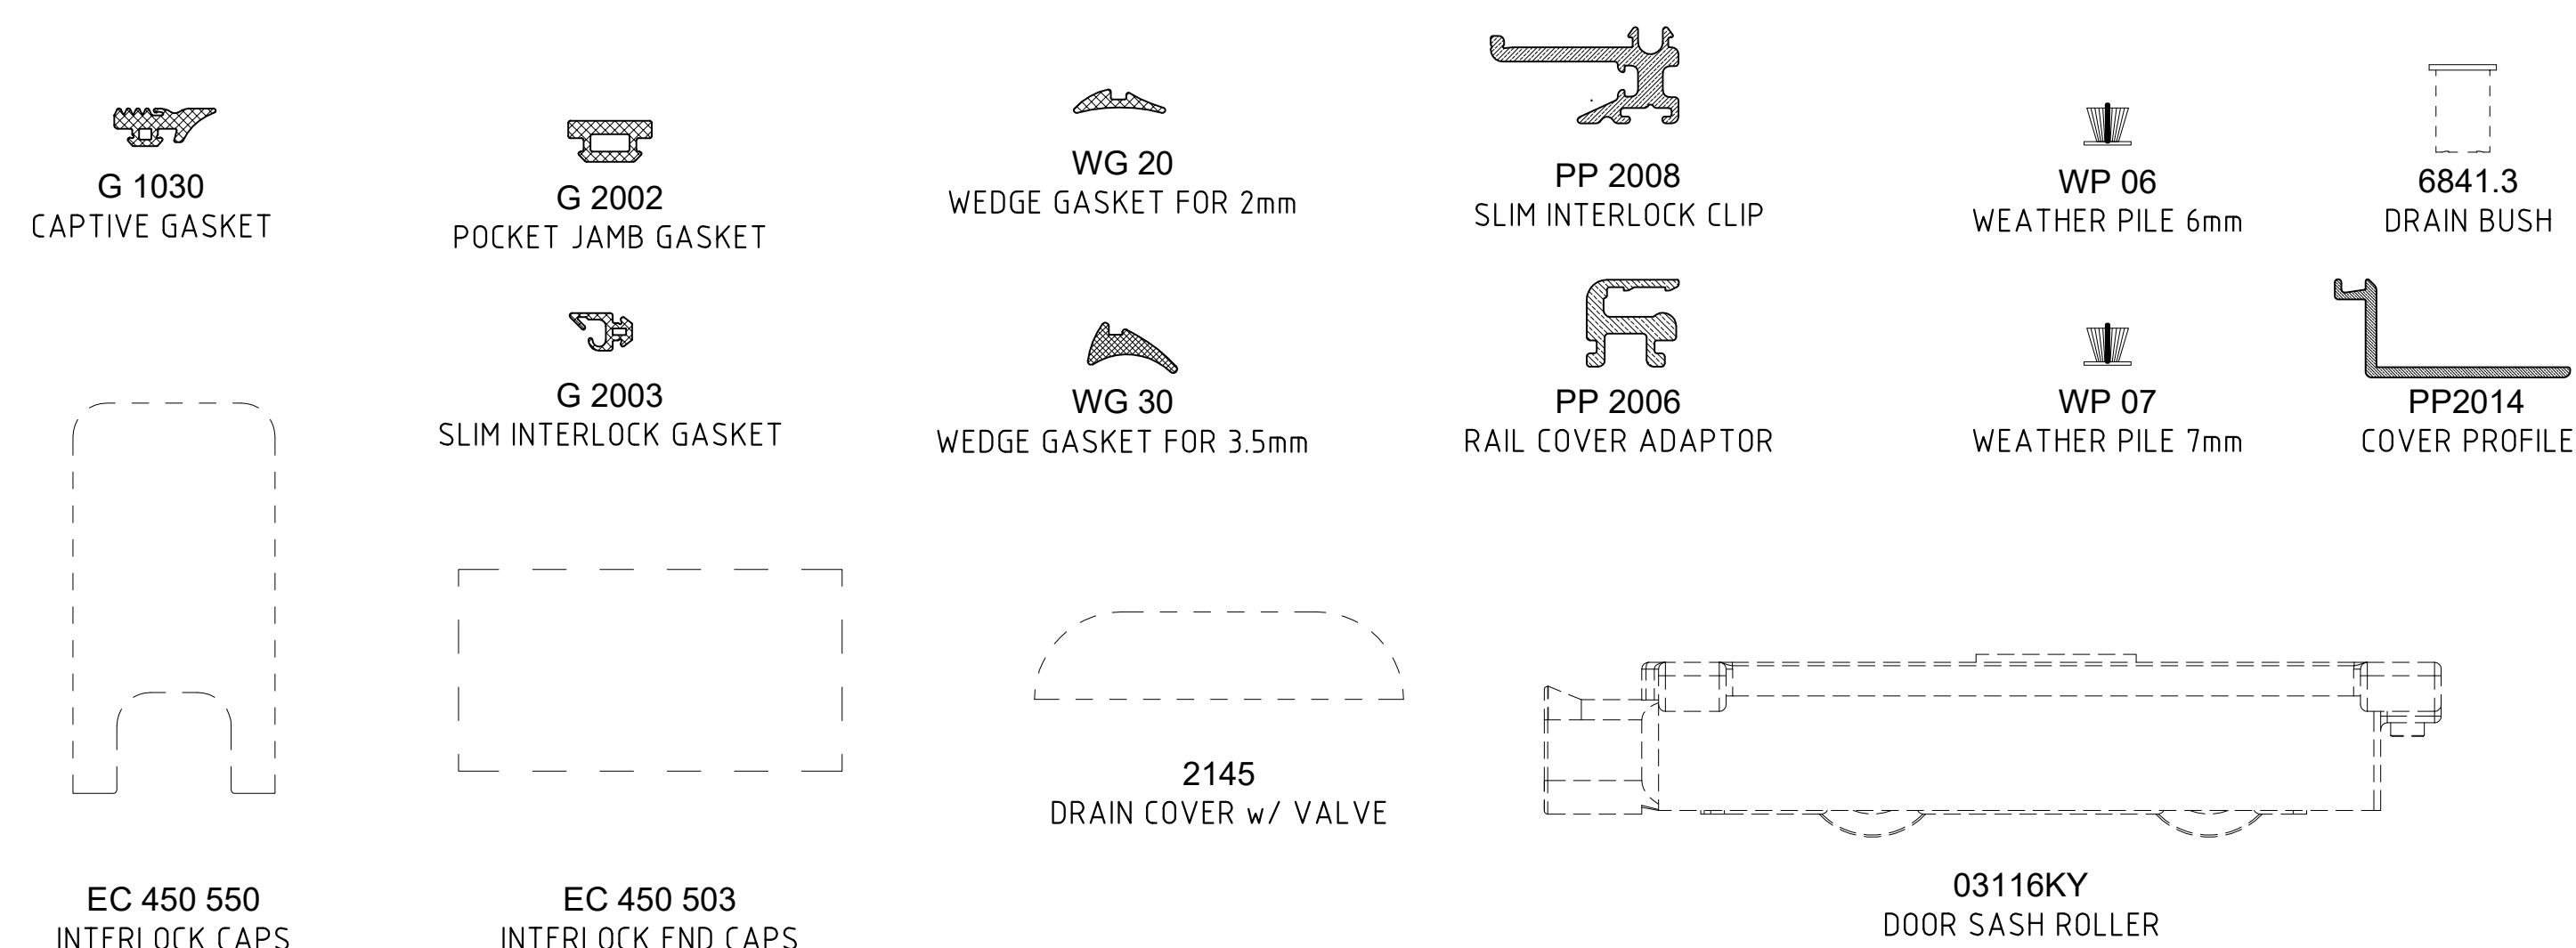

Project : AJMAN CREEK TOWERS , Rashidia 01, Ajman U.A.E.

Consultant : **CANADIAN** **المكتب الكندي**
CONSULTANT **المستشارت الهندسية**

Client : Mr. Ghaleb Kamel Jaber

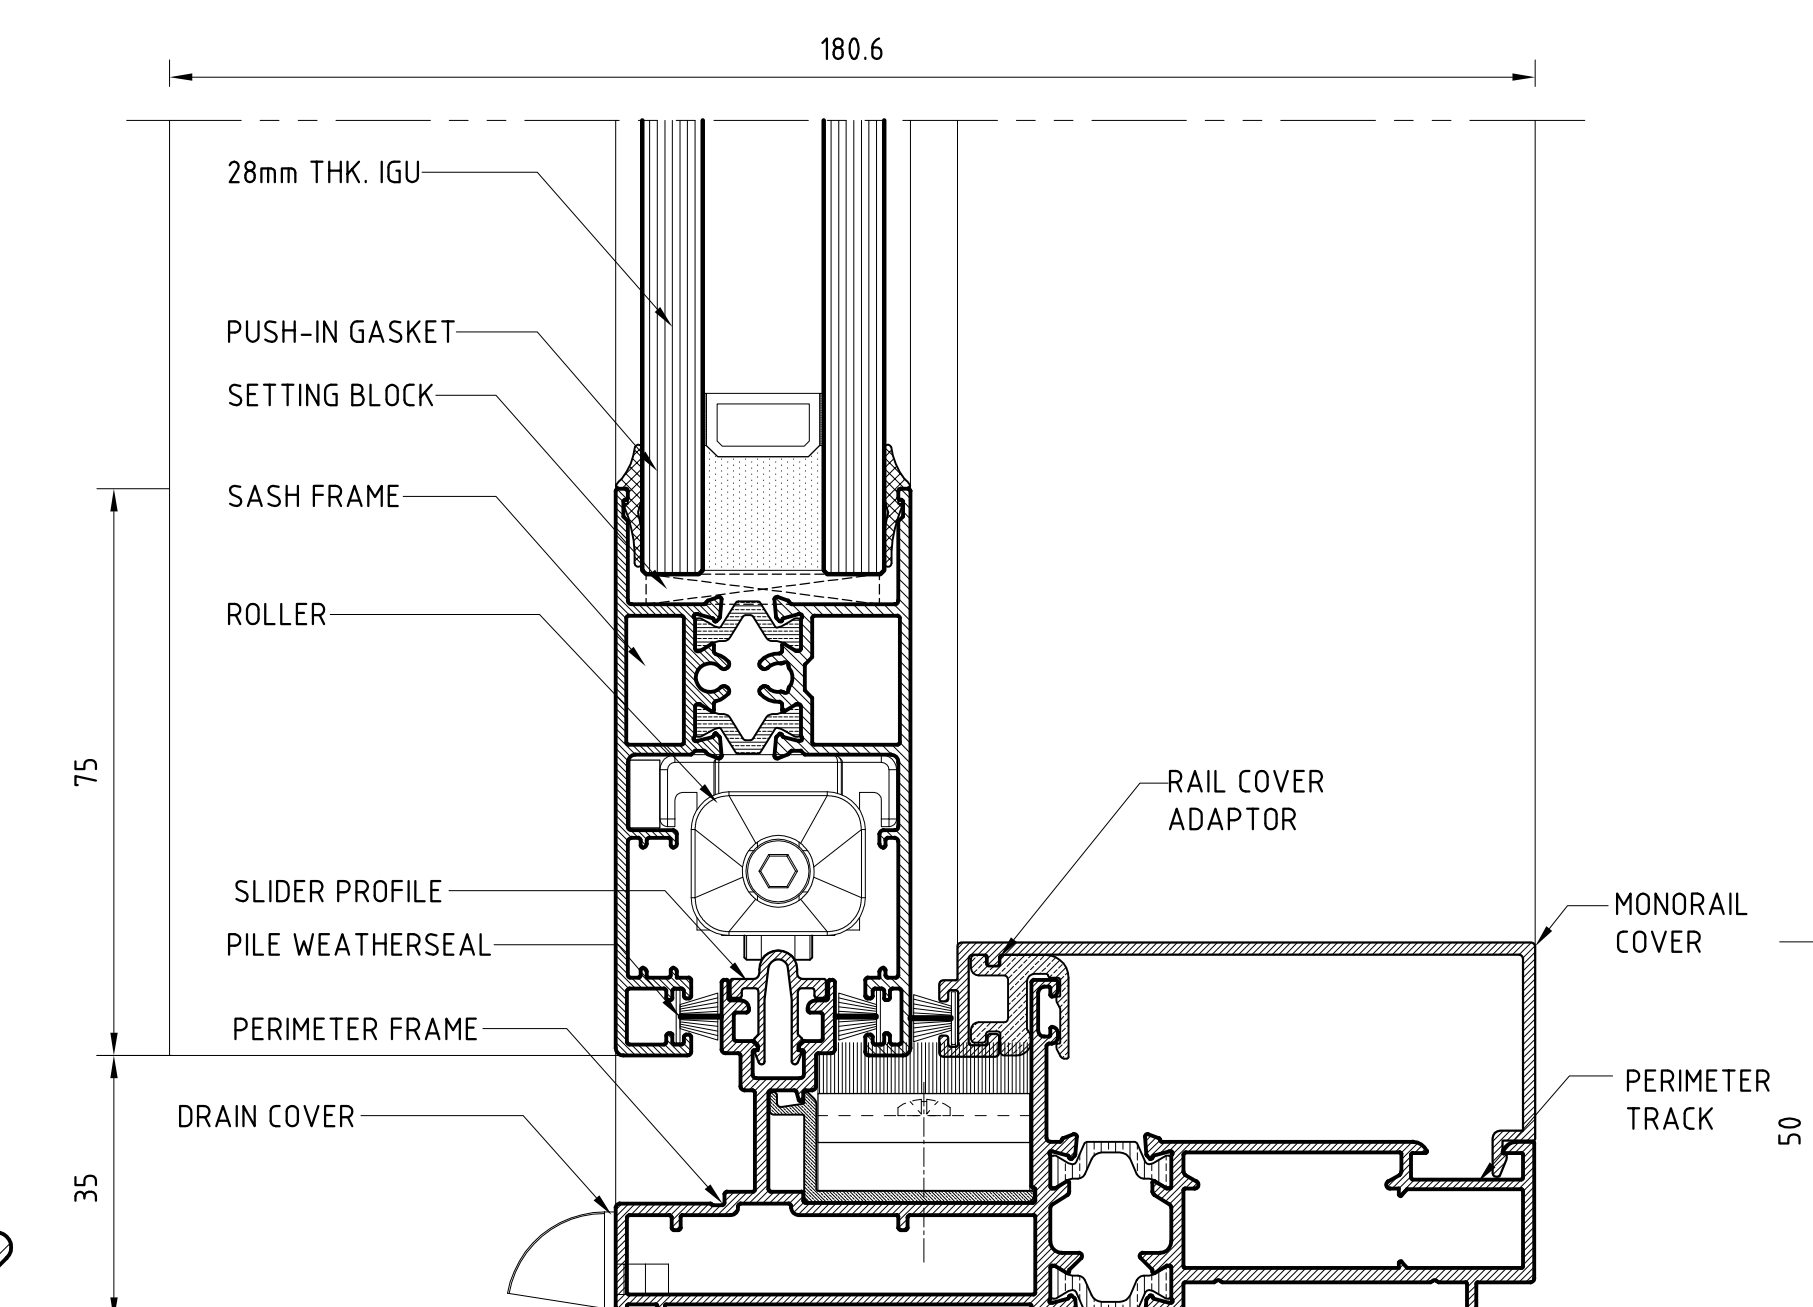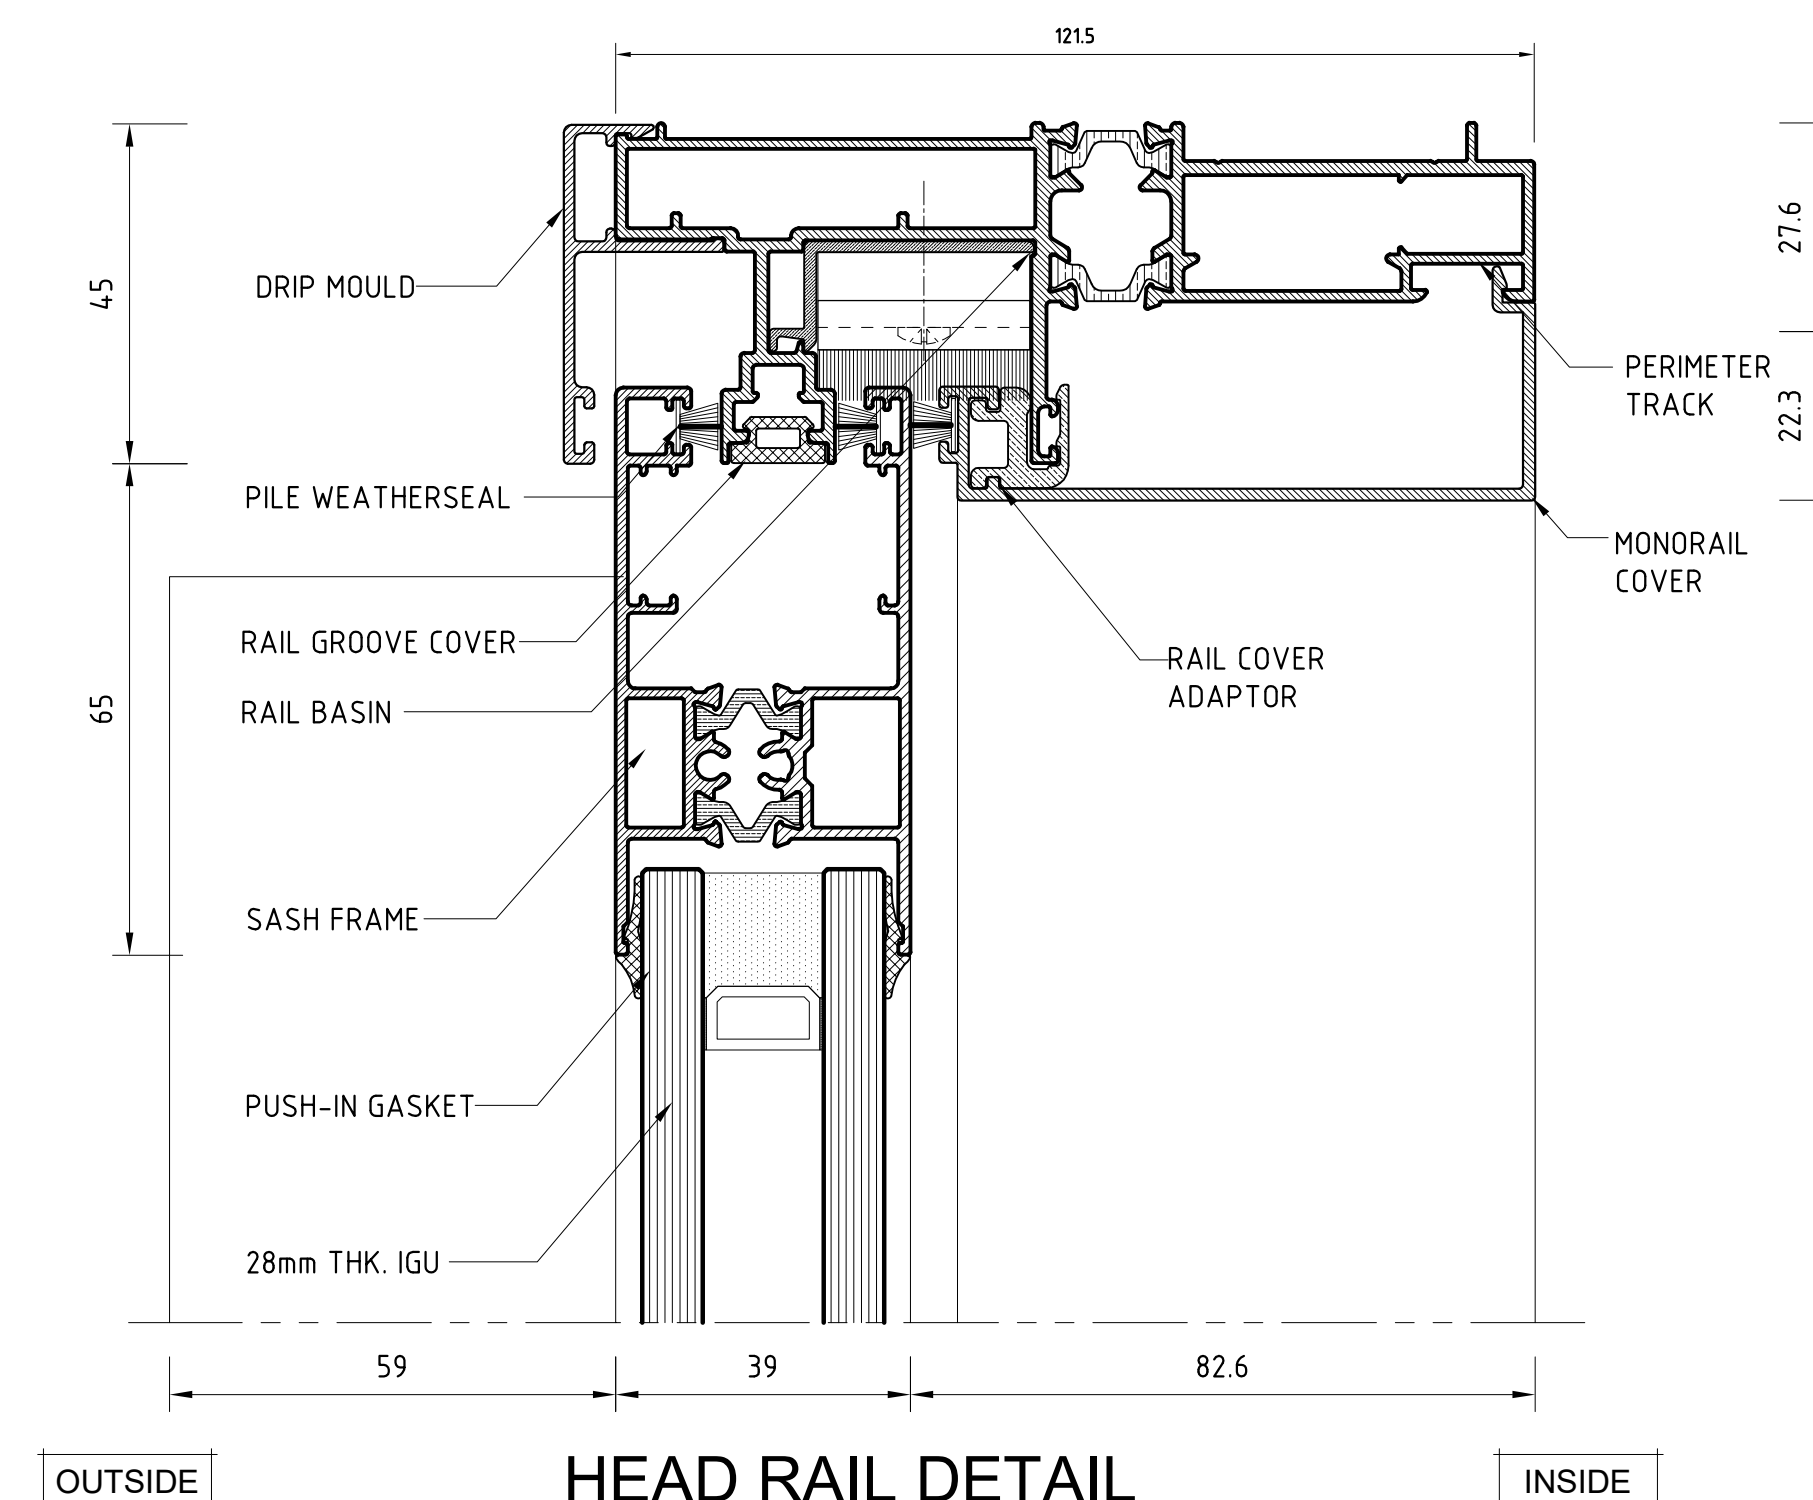

BOTTOM RAIL DETAIL