
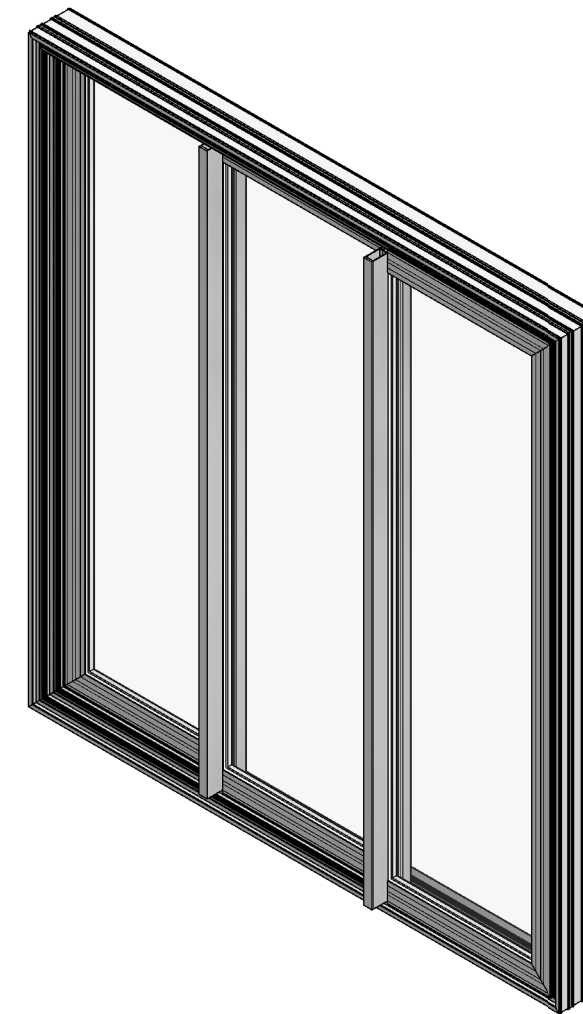
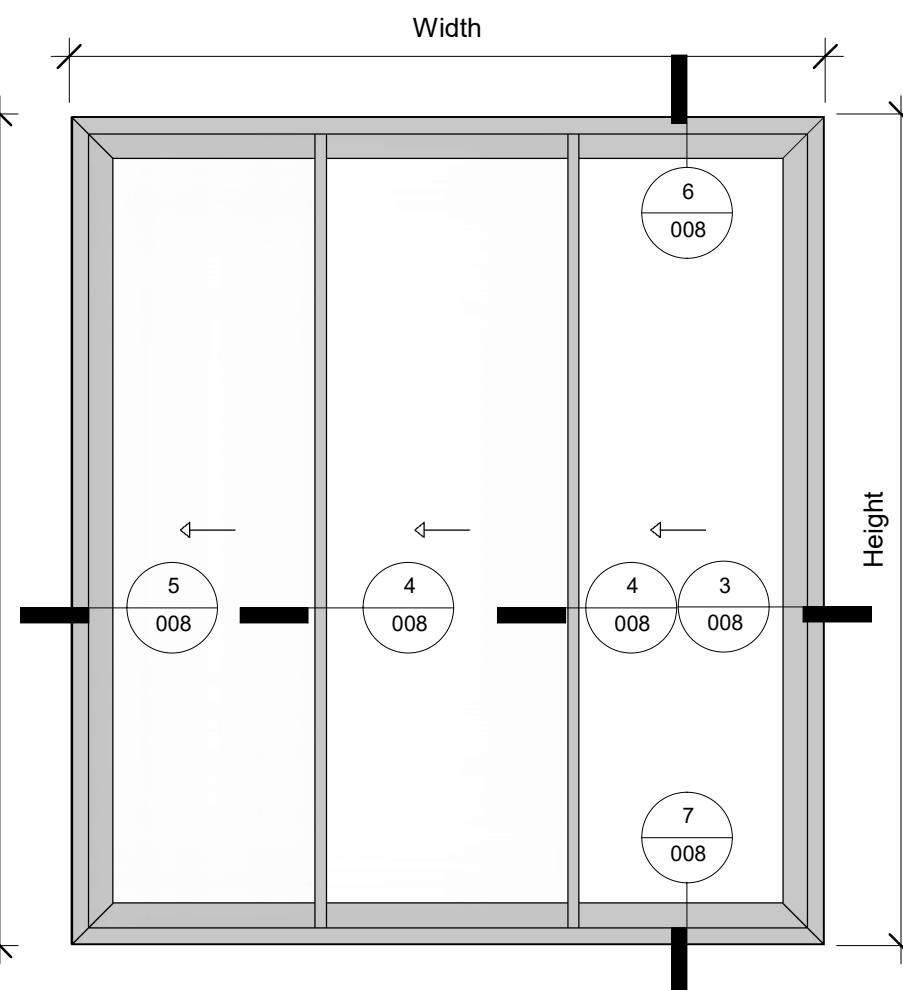


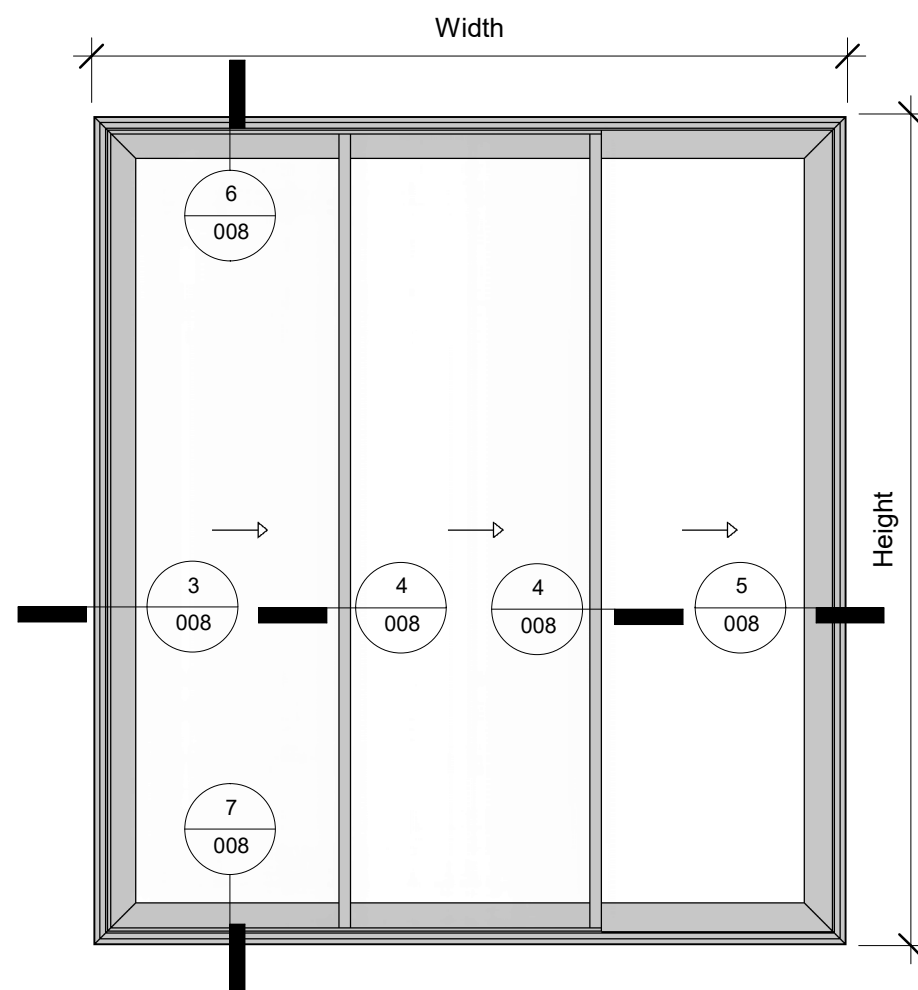

GERMAN ENGINEERING SINCE 1967

SYKON 

 GmbH

NOTE:
* All dimensions are in mm. unless otherwise specified.

CONSULTANT/CLIENT APPROVAL			
No.	STATUS		DATE
A	APPROVED		
B	APPROVED AS NOTED		
C	NOT APPROVED, RESUBMIT		
D	INCOMPLETE, RESUBMIT		
REV.	DESCRIPTION	CHKD	DATE
00	Revision 00		10/09/2024
01	Revision 01		05/11/2024

PROJECT PICTURE:

PROJECT:

CONSULTANT:

CLIENT:

DRAWING CONTENT:

SL450s 3 Track Sliding Door

DRAWN: SJ	DATE: 05.11.2024	SYSTEM SL450
CHECKED: MK	SCALE: As indicated	
DRAWING No. 008		REV. No. 01

