

NOTE:  
\* All dimensions are in mm. unless otherwise specified.

| CONSULTANT/CLIENT APPROVAL |                        |      |            |
|----------------------------|------------------------|------|------------|
| No.                        | STATUS                 | DATE |            |
| A                          | APPROVED               |      |            |
| B                          | APPROVED AS NOTED      |      |            |
| C                          | NOT APPROVED, RESUBMIT |      |            |
| D                          | INCOMPLETE, RESUBMIT   |      |            |
| REV.                       | DESCRIPTION            | CHKD | DATE       |
| 00                         | Revision 00            |      | 10/09/2024 |
| 01                         | Revision 01            |      | 05/11/2024 |
|                            |                        |      |            |

PROJECT PICTURE:

PROJECT:

CONSULTANT:


CLIENT:

DRAWING CONTENT:


SY35 Top Hung Window  
Wall Fix

|                |                        |                       |
|----------------|------------------------|-----------------------|
| DRAWN:<br>SJ   | DATE:<br>05.11.2024    | SYSTEM<br><b>SY35</b> |
| CHECKED:<br>MK | SCALE:<br>As indicated |                       |


|             |          |
|-------------|----------|
| DRAWING No. | REV. No. |
| 013         | 01       |

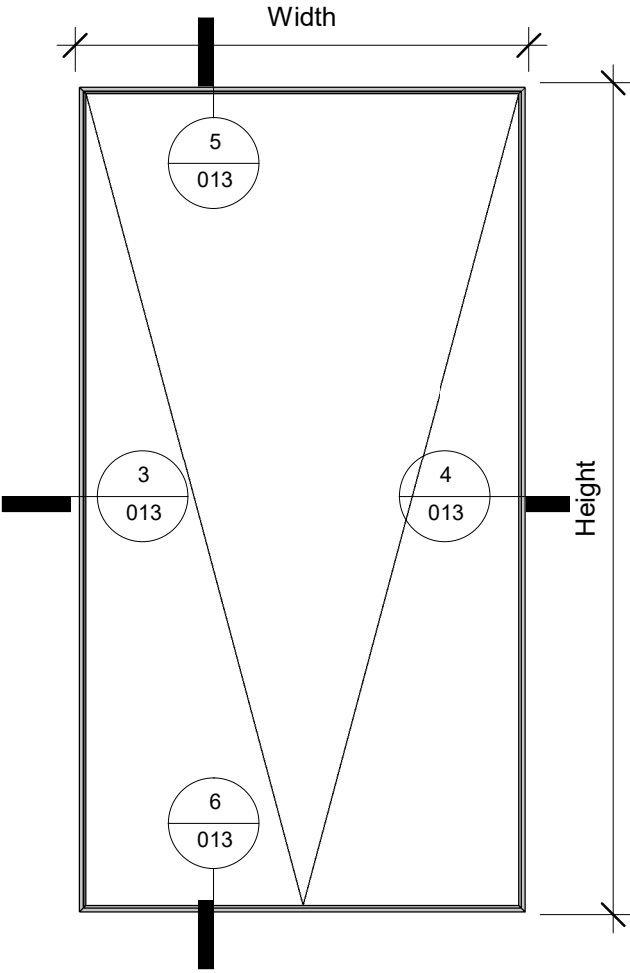


1 Elevation Front  
1 : 20

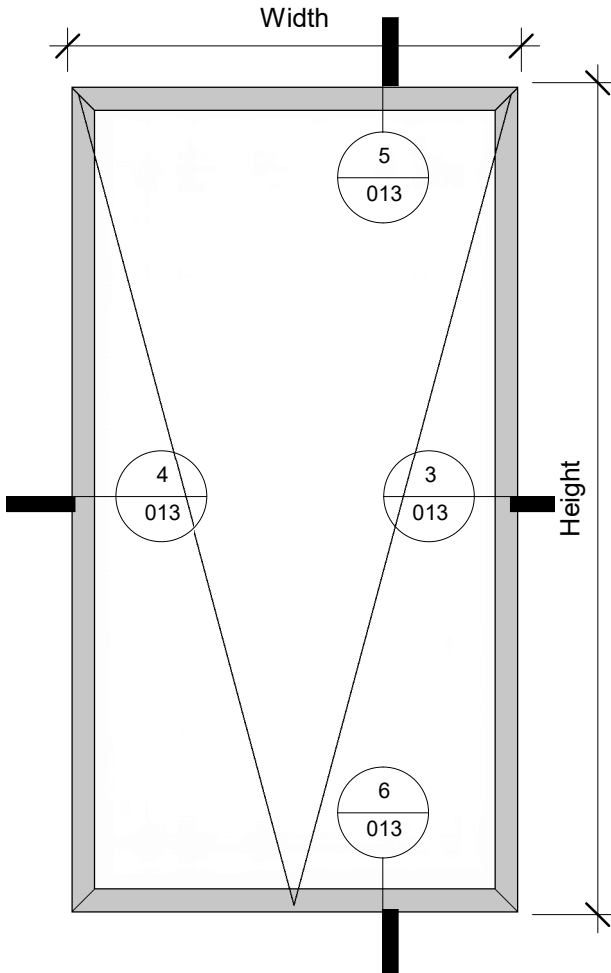


2 Elevation Back  
1 : 20

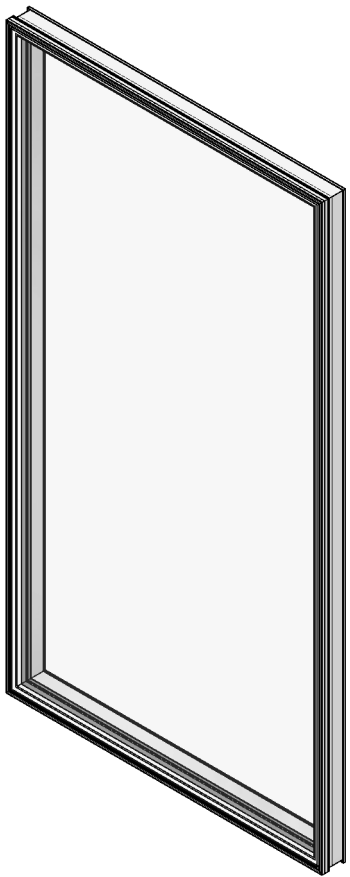


7 3D View

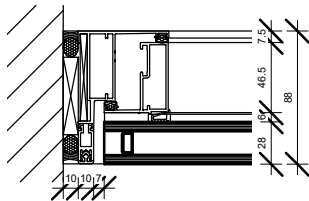


3 Detail 1  
1 : 5

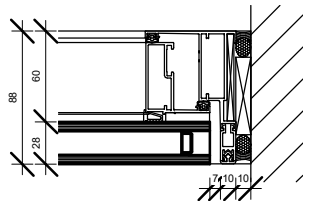

4 Detail 2  
1 : 5

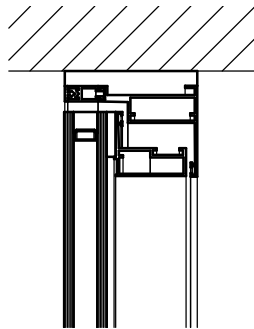

5 Detail 3  
1 : 5

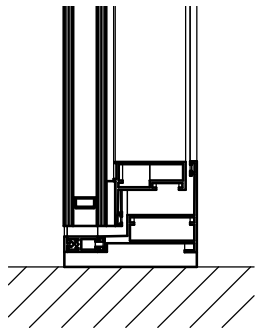

6 Detail 4  
1 : 5