



SY 50 Stick Curtain Wall (Toggle Glazed)

CERTIFICATIONS


- Air Infiltration & Exfiltration (ASTM E283/E283M-19) 600 Pa
- Water Penetration (ASTM E331-00 Reapproved 2016) 750 Pa
- Wind Resistance Serviceability (ASTM E330/E330M-14) 2000 Pa
- Wind Resistance Safety (ASTM E330/E330M-14) 4500 Pa
- Maximum Glass Thickness that can be accommodated is 54mm

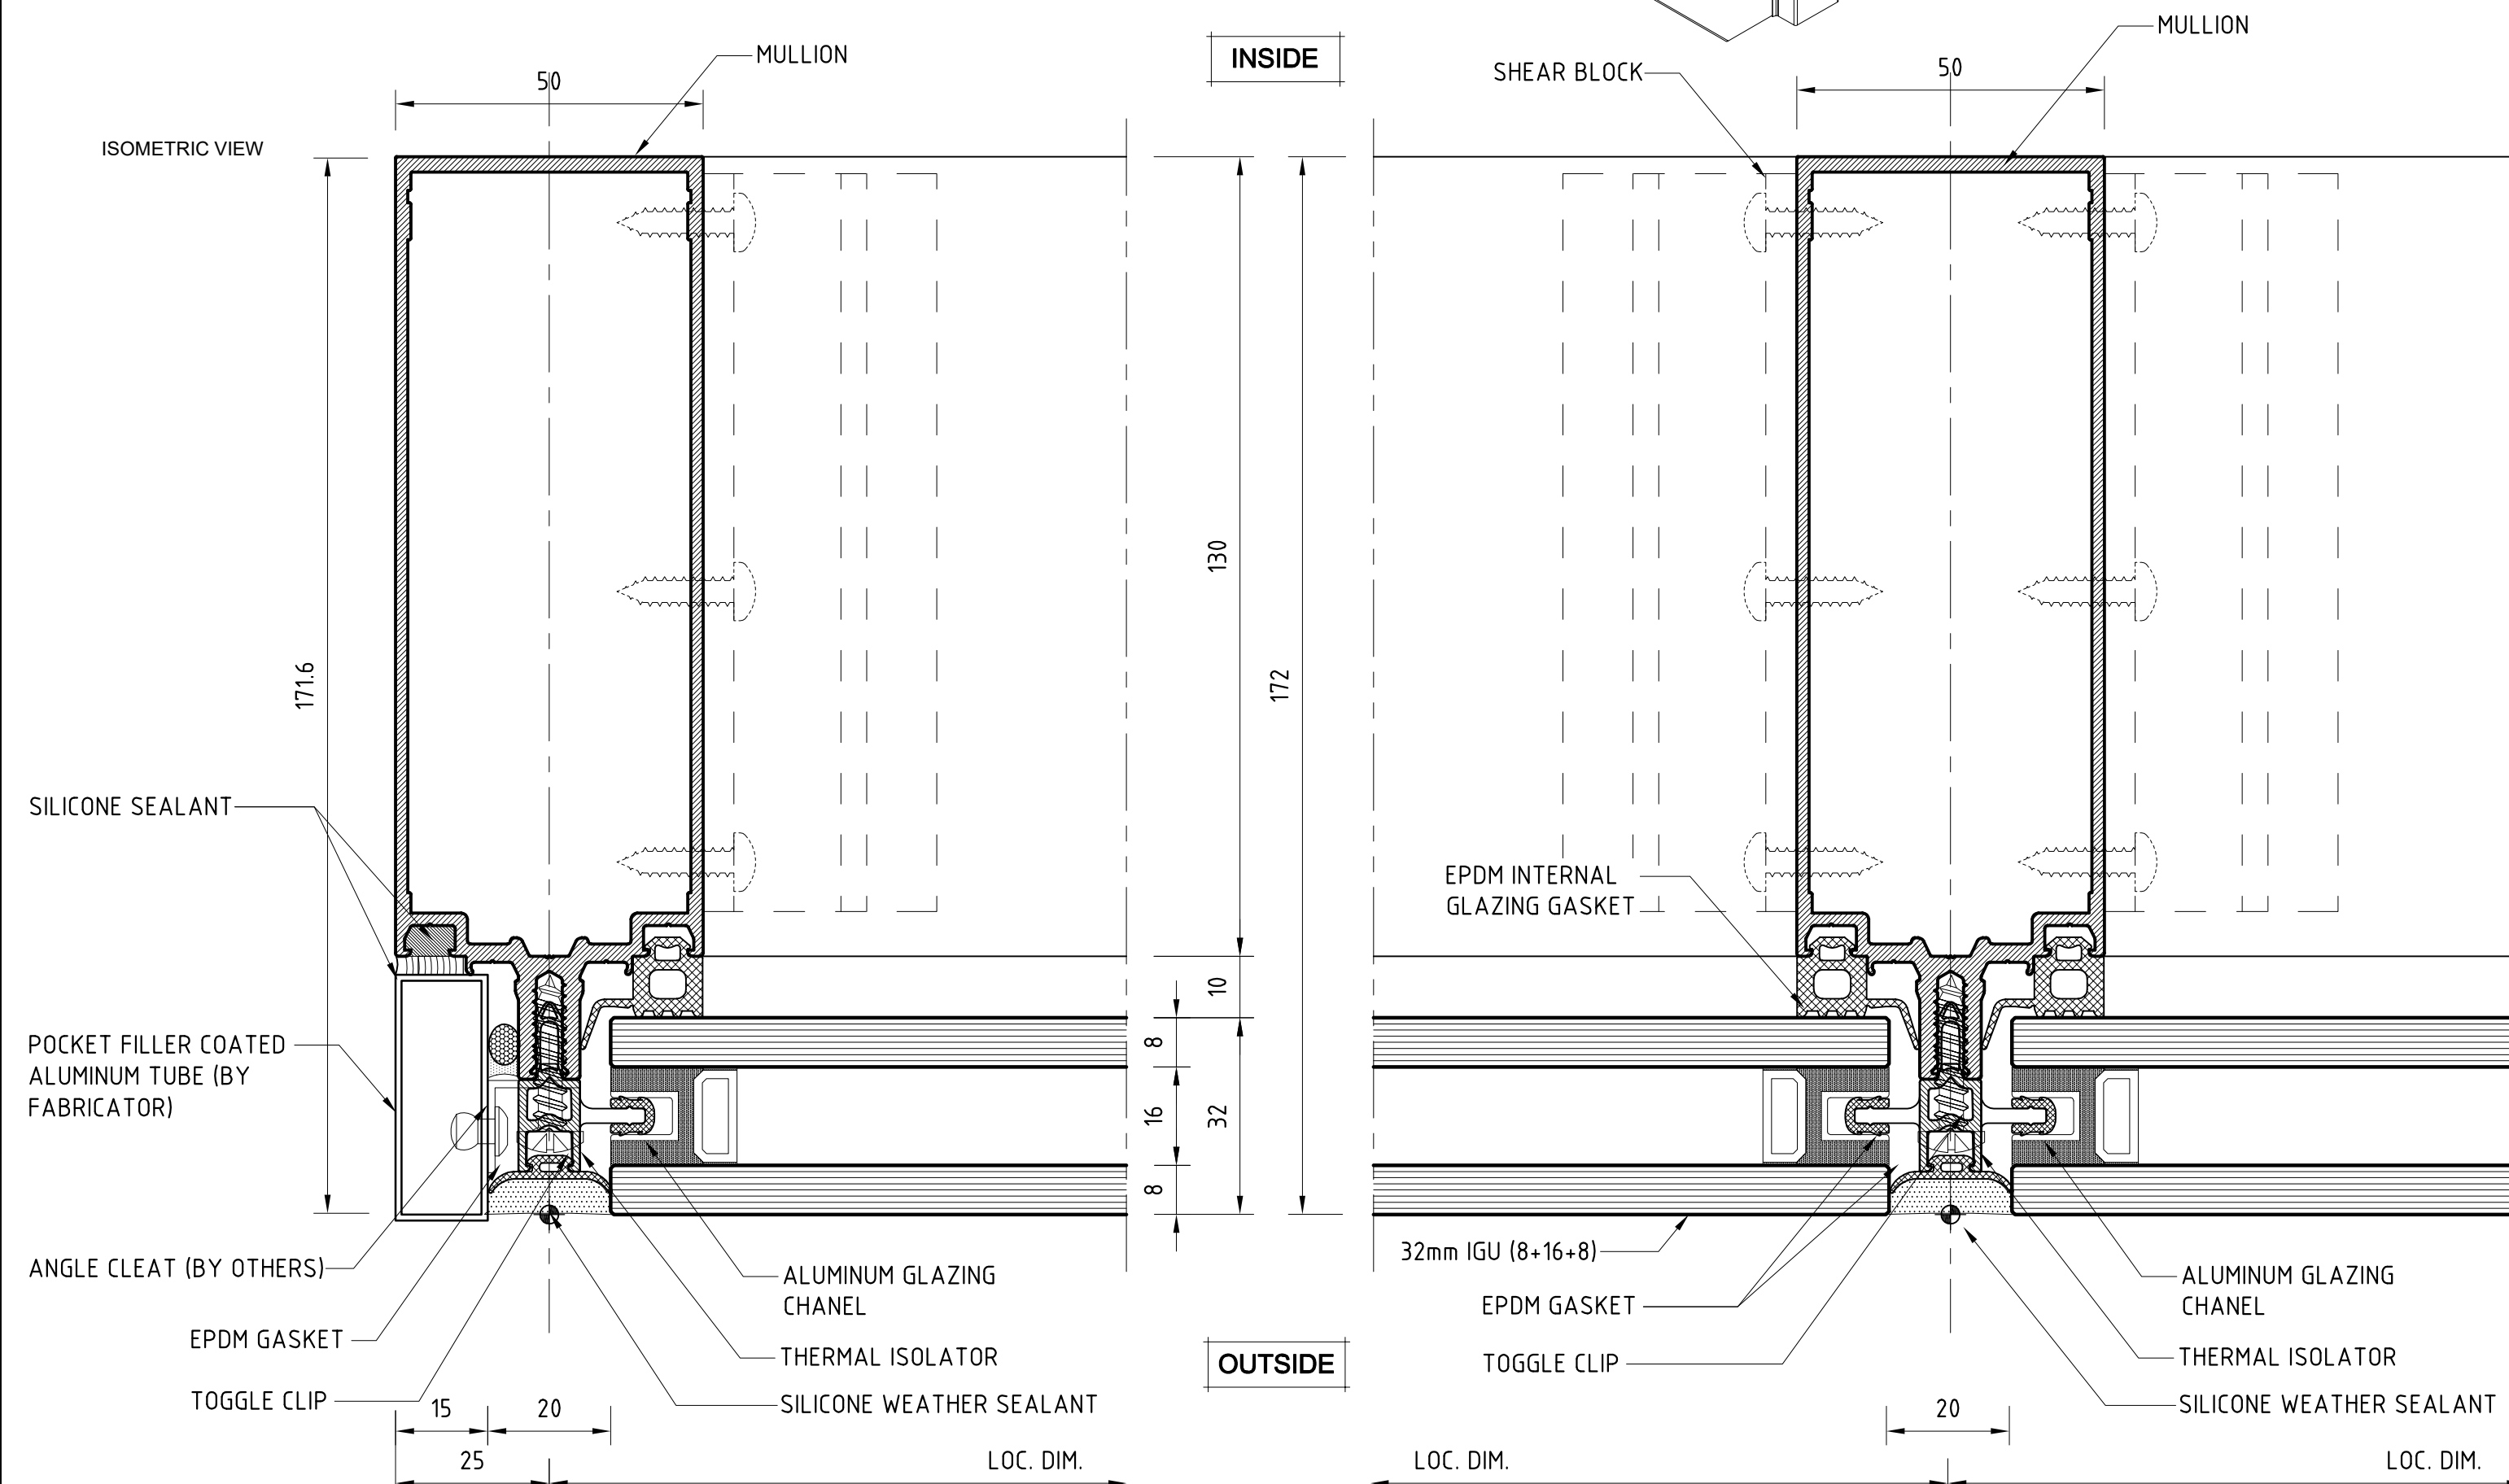






JAMB MULLION DETAIL

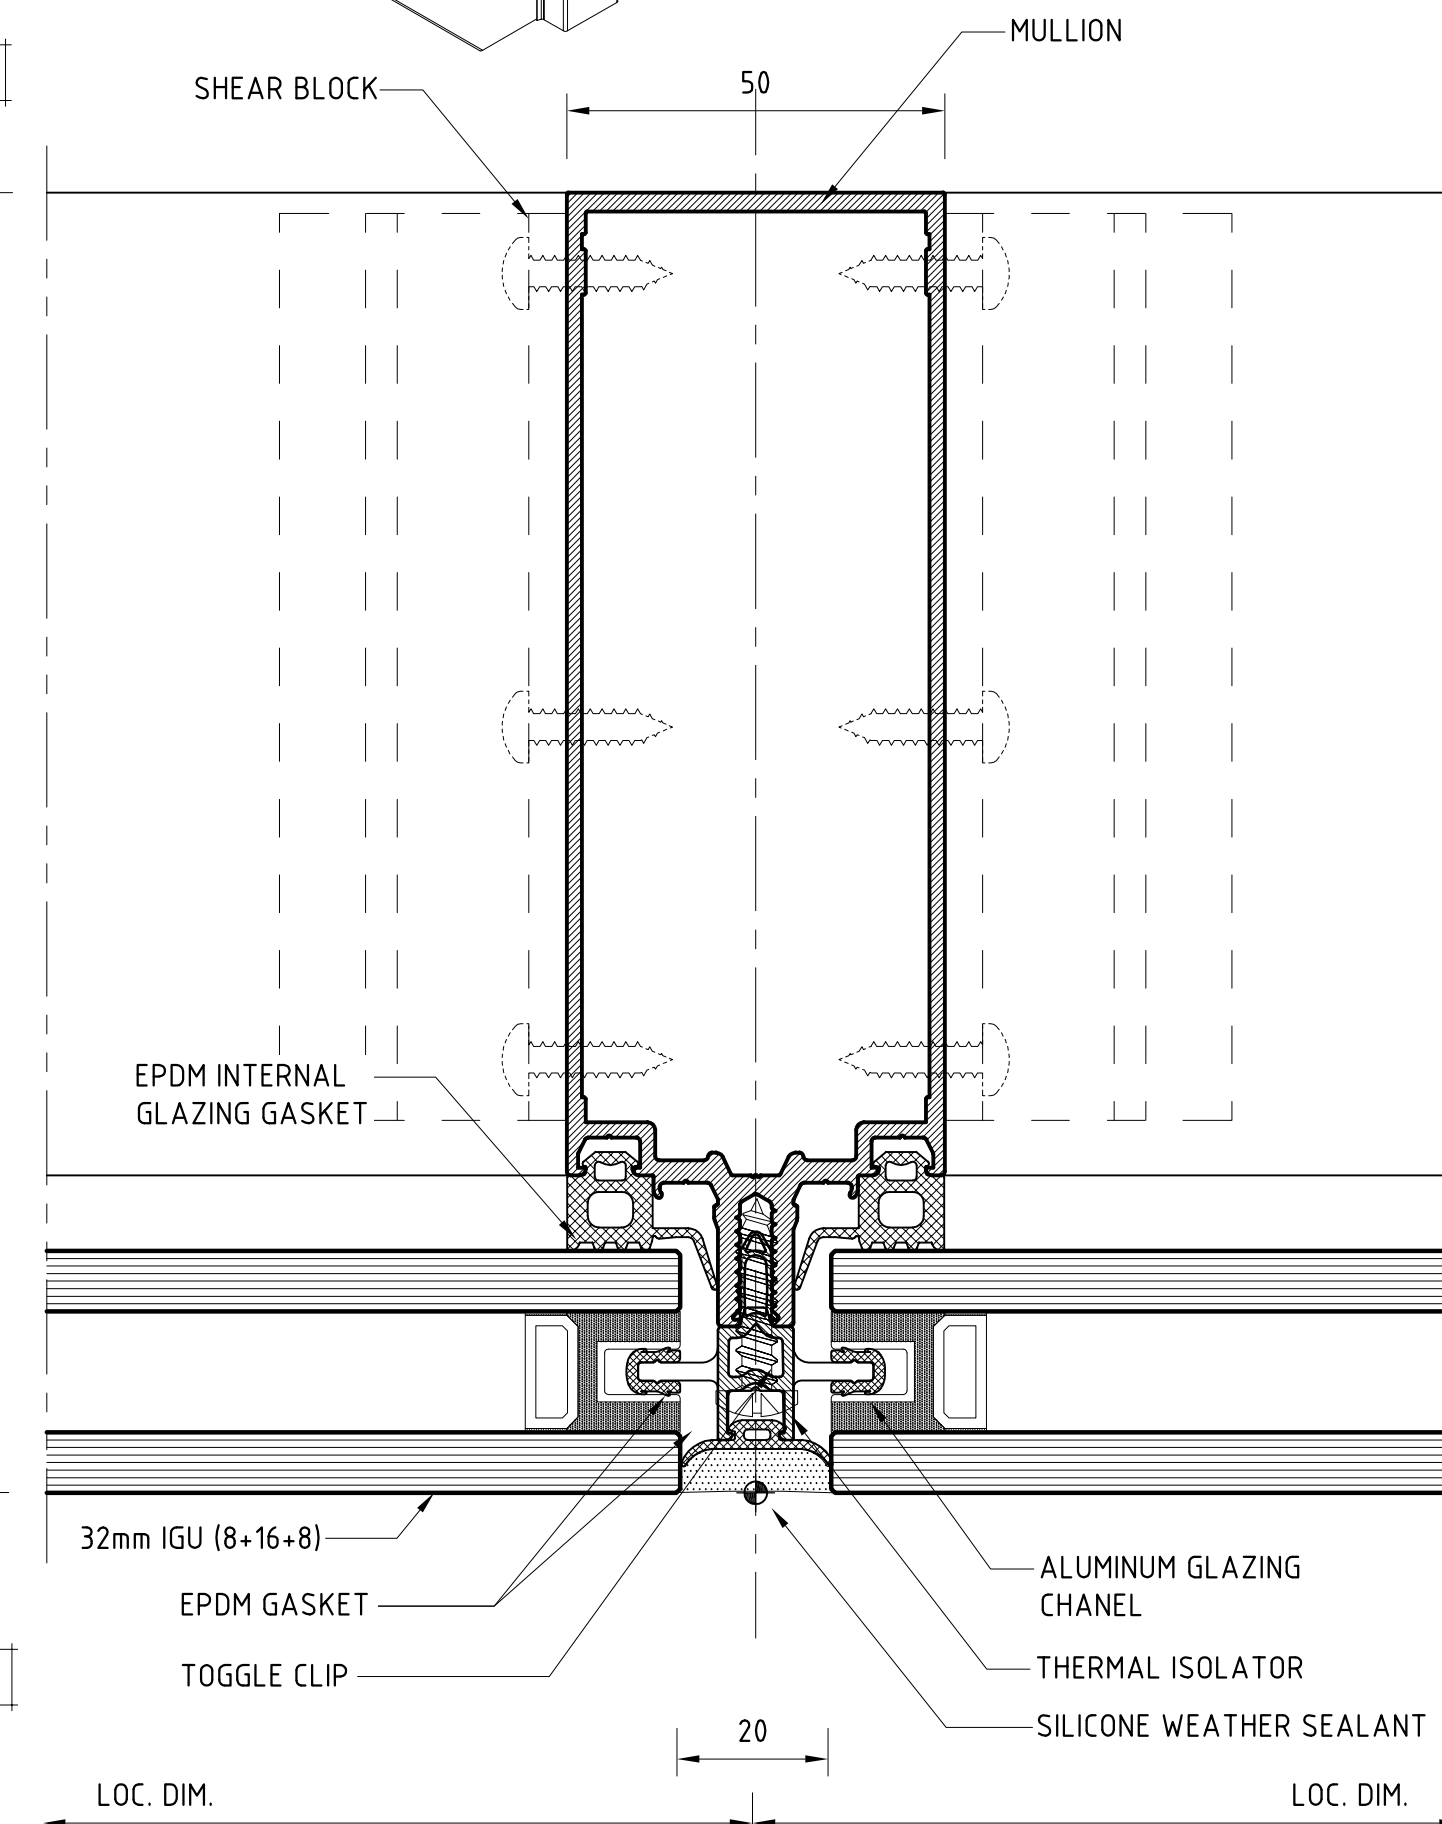

INTERMEDIATE MULLION DETAIL

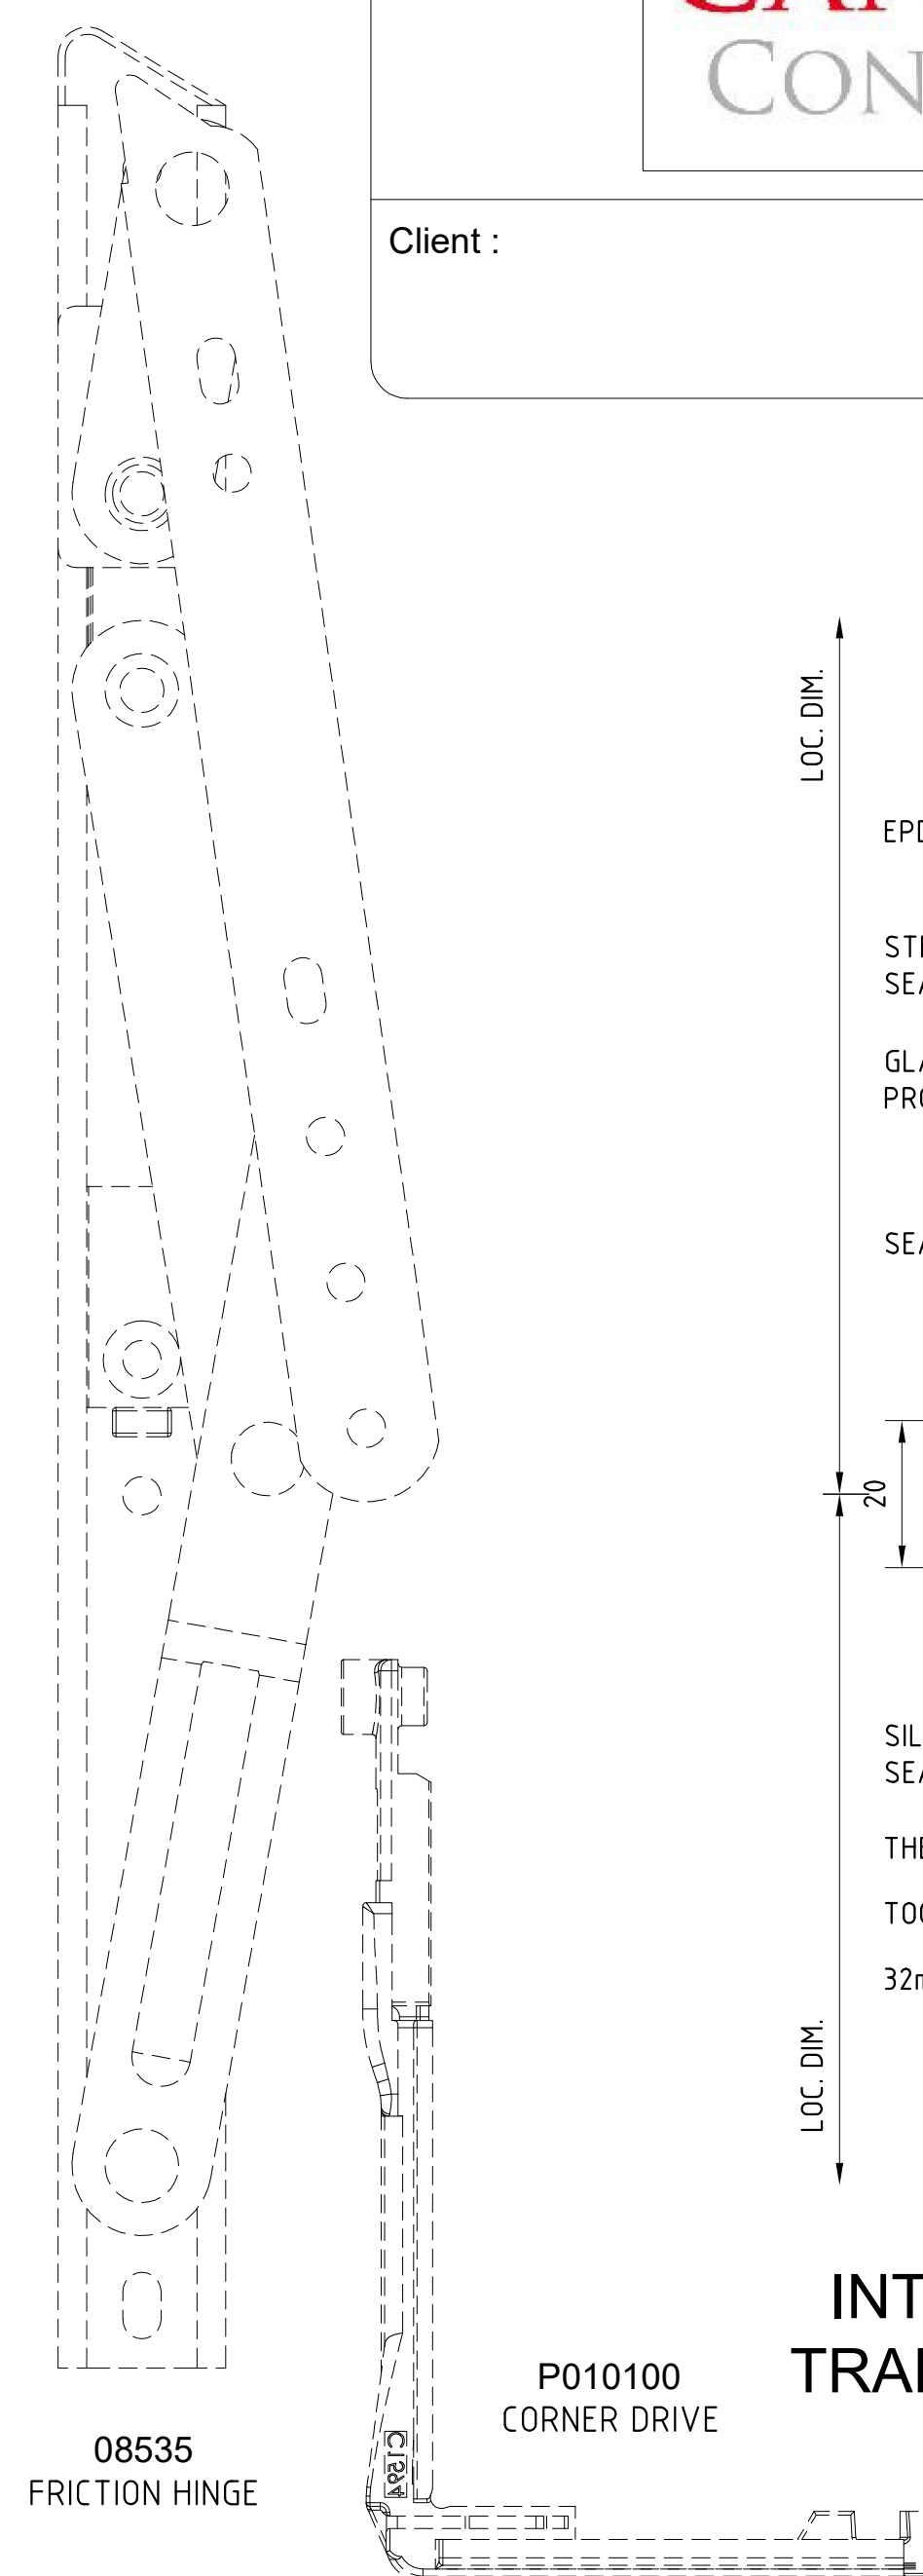

INTERMEDIATE
TRANSOM DETAIL

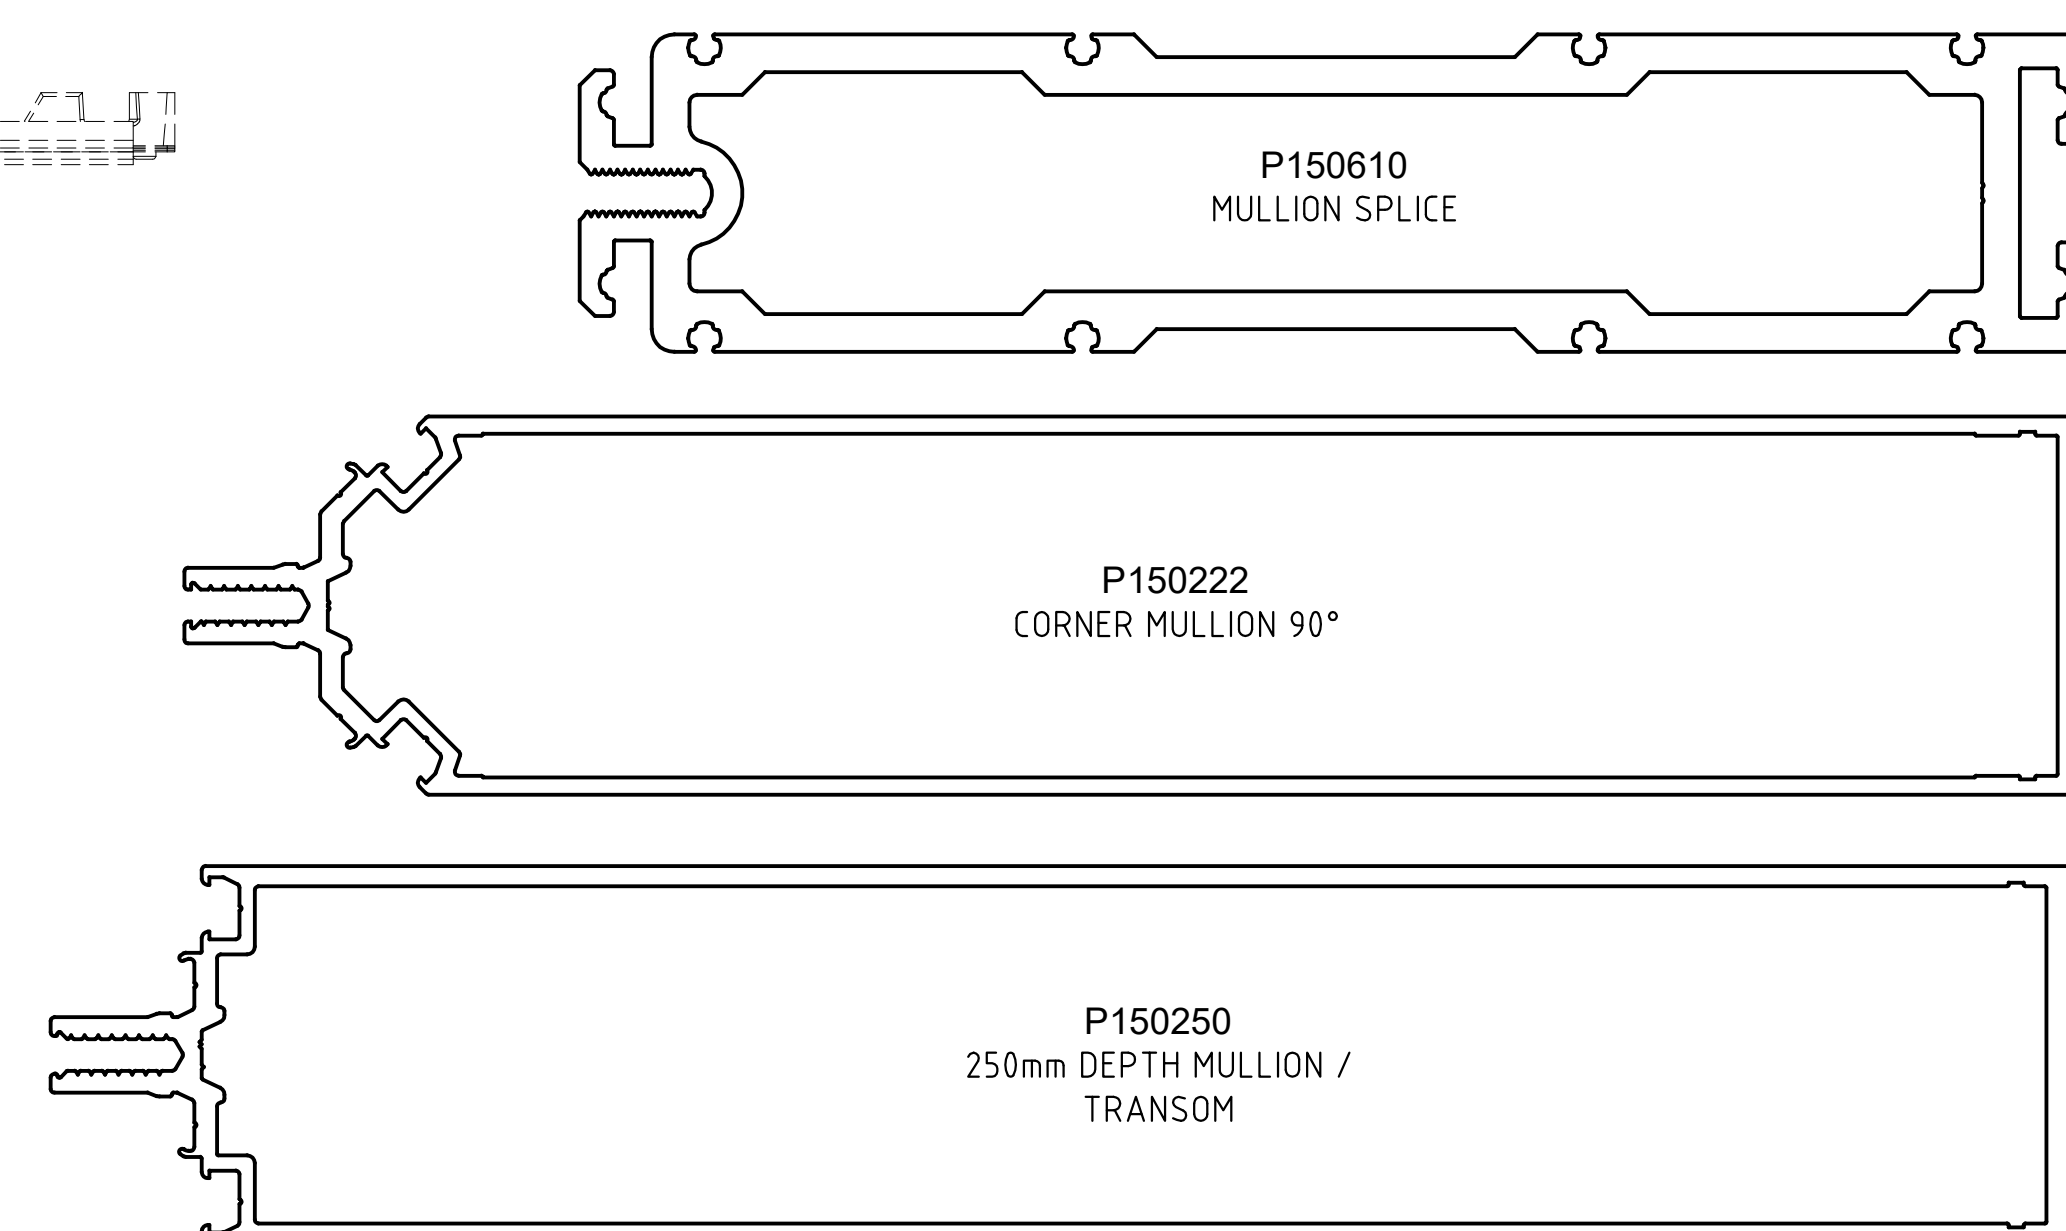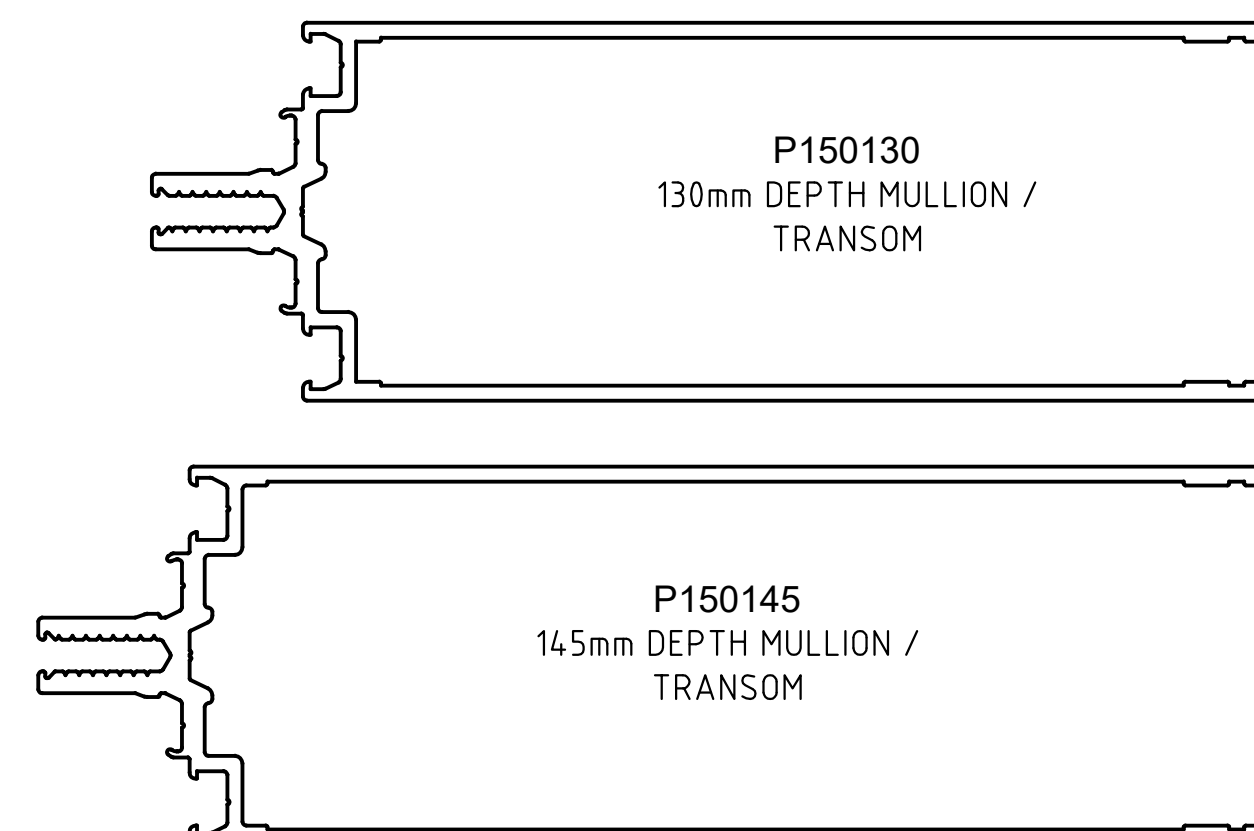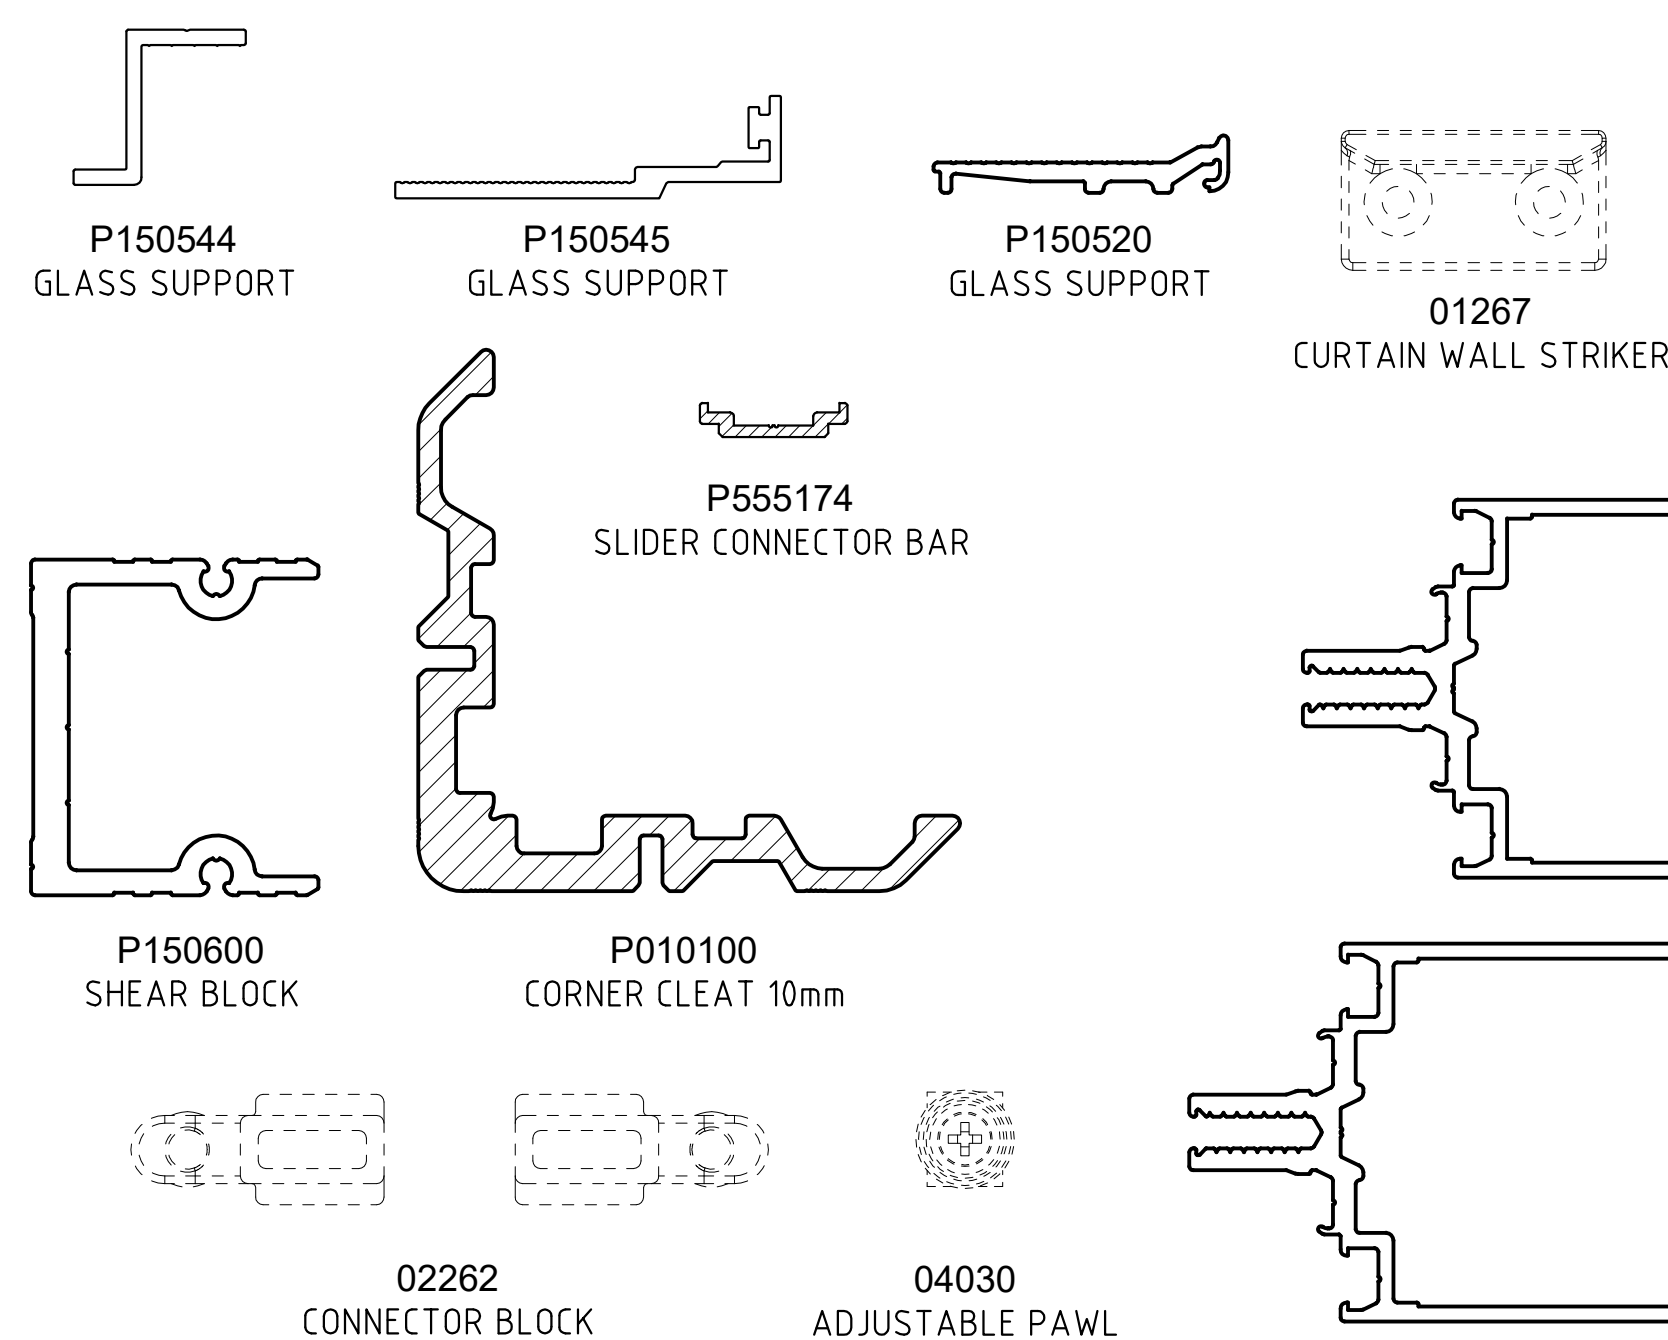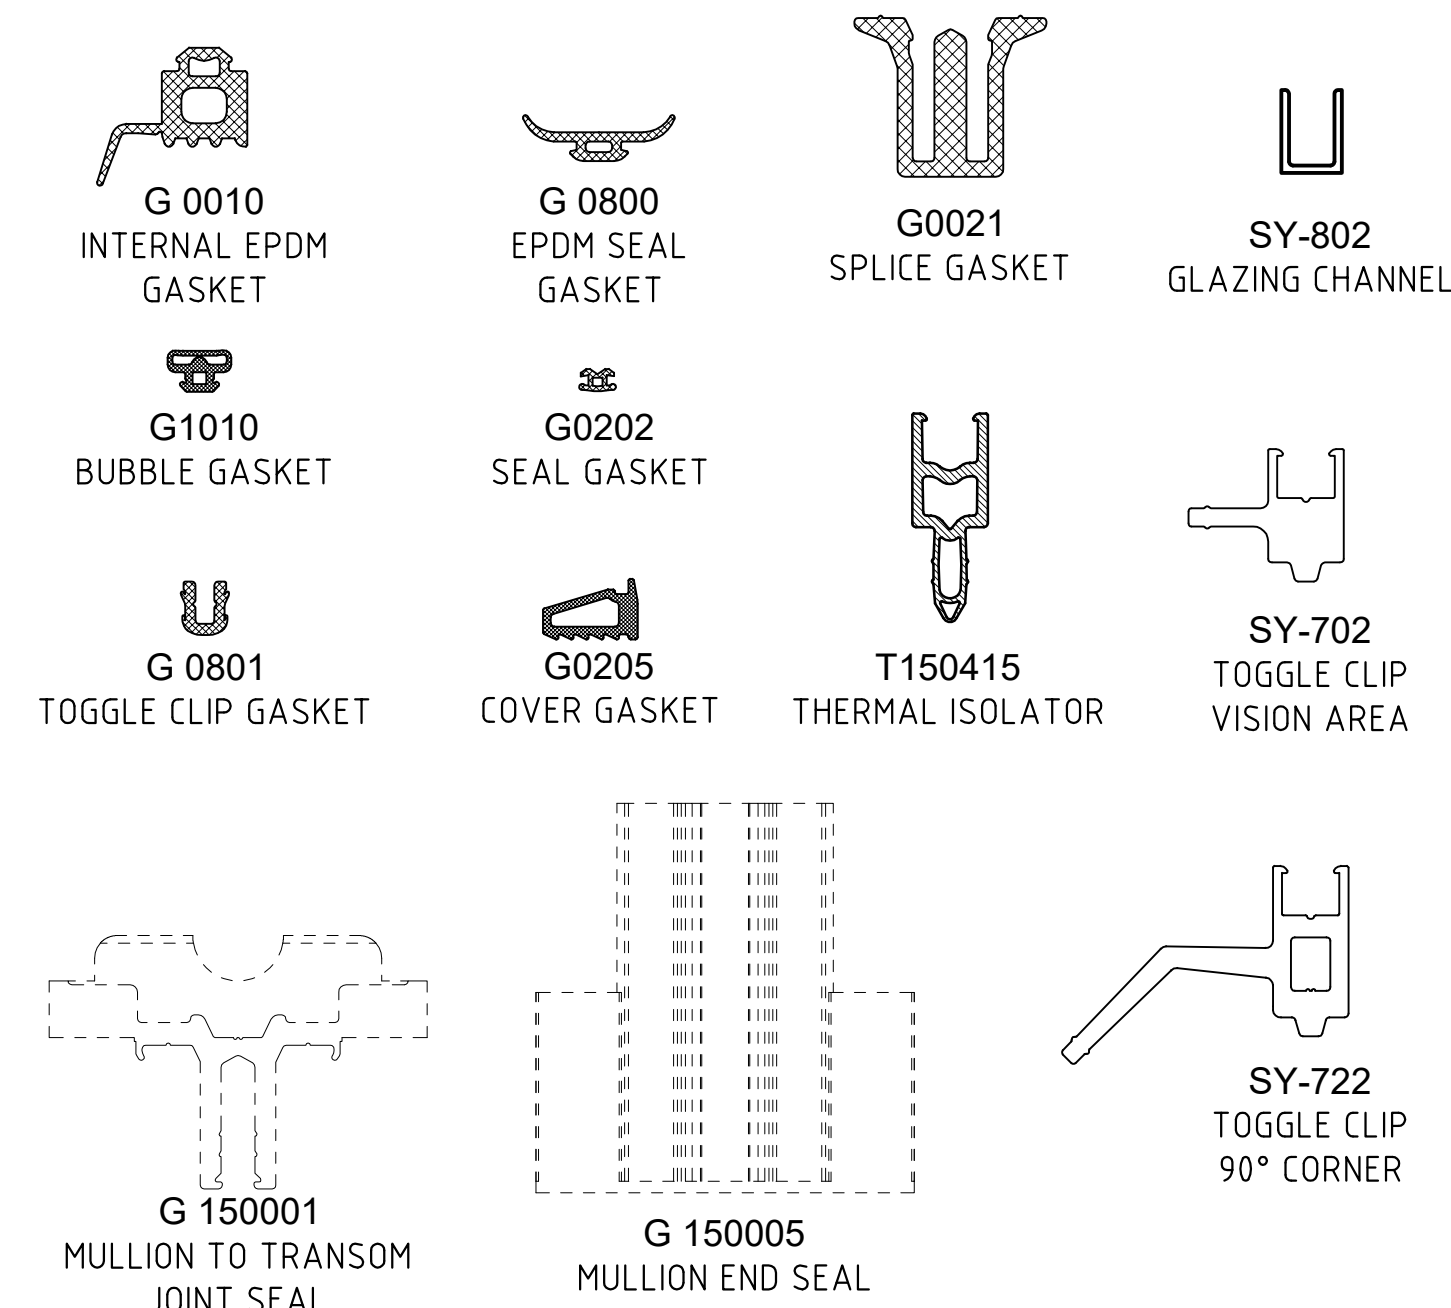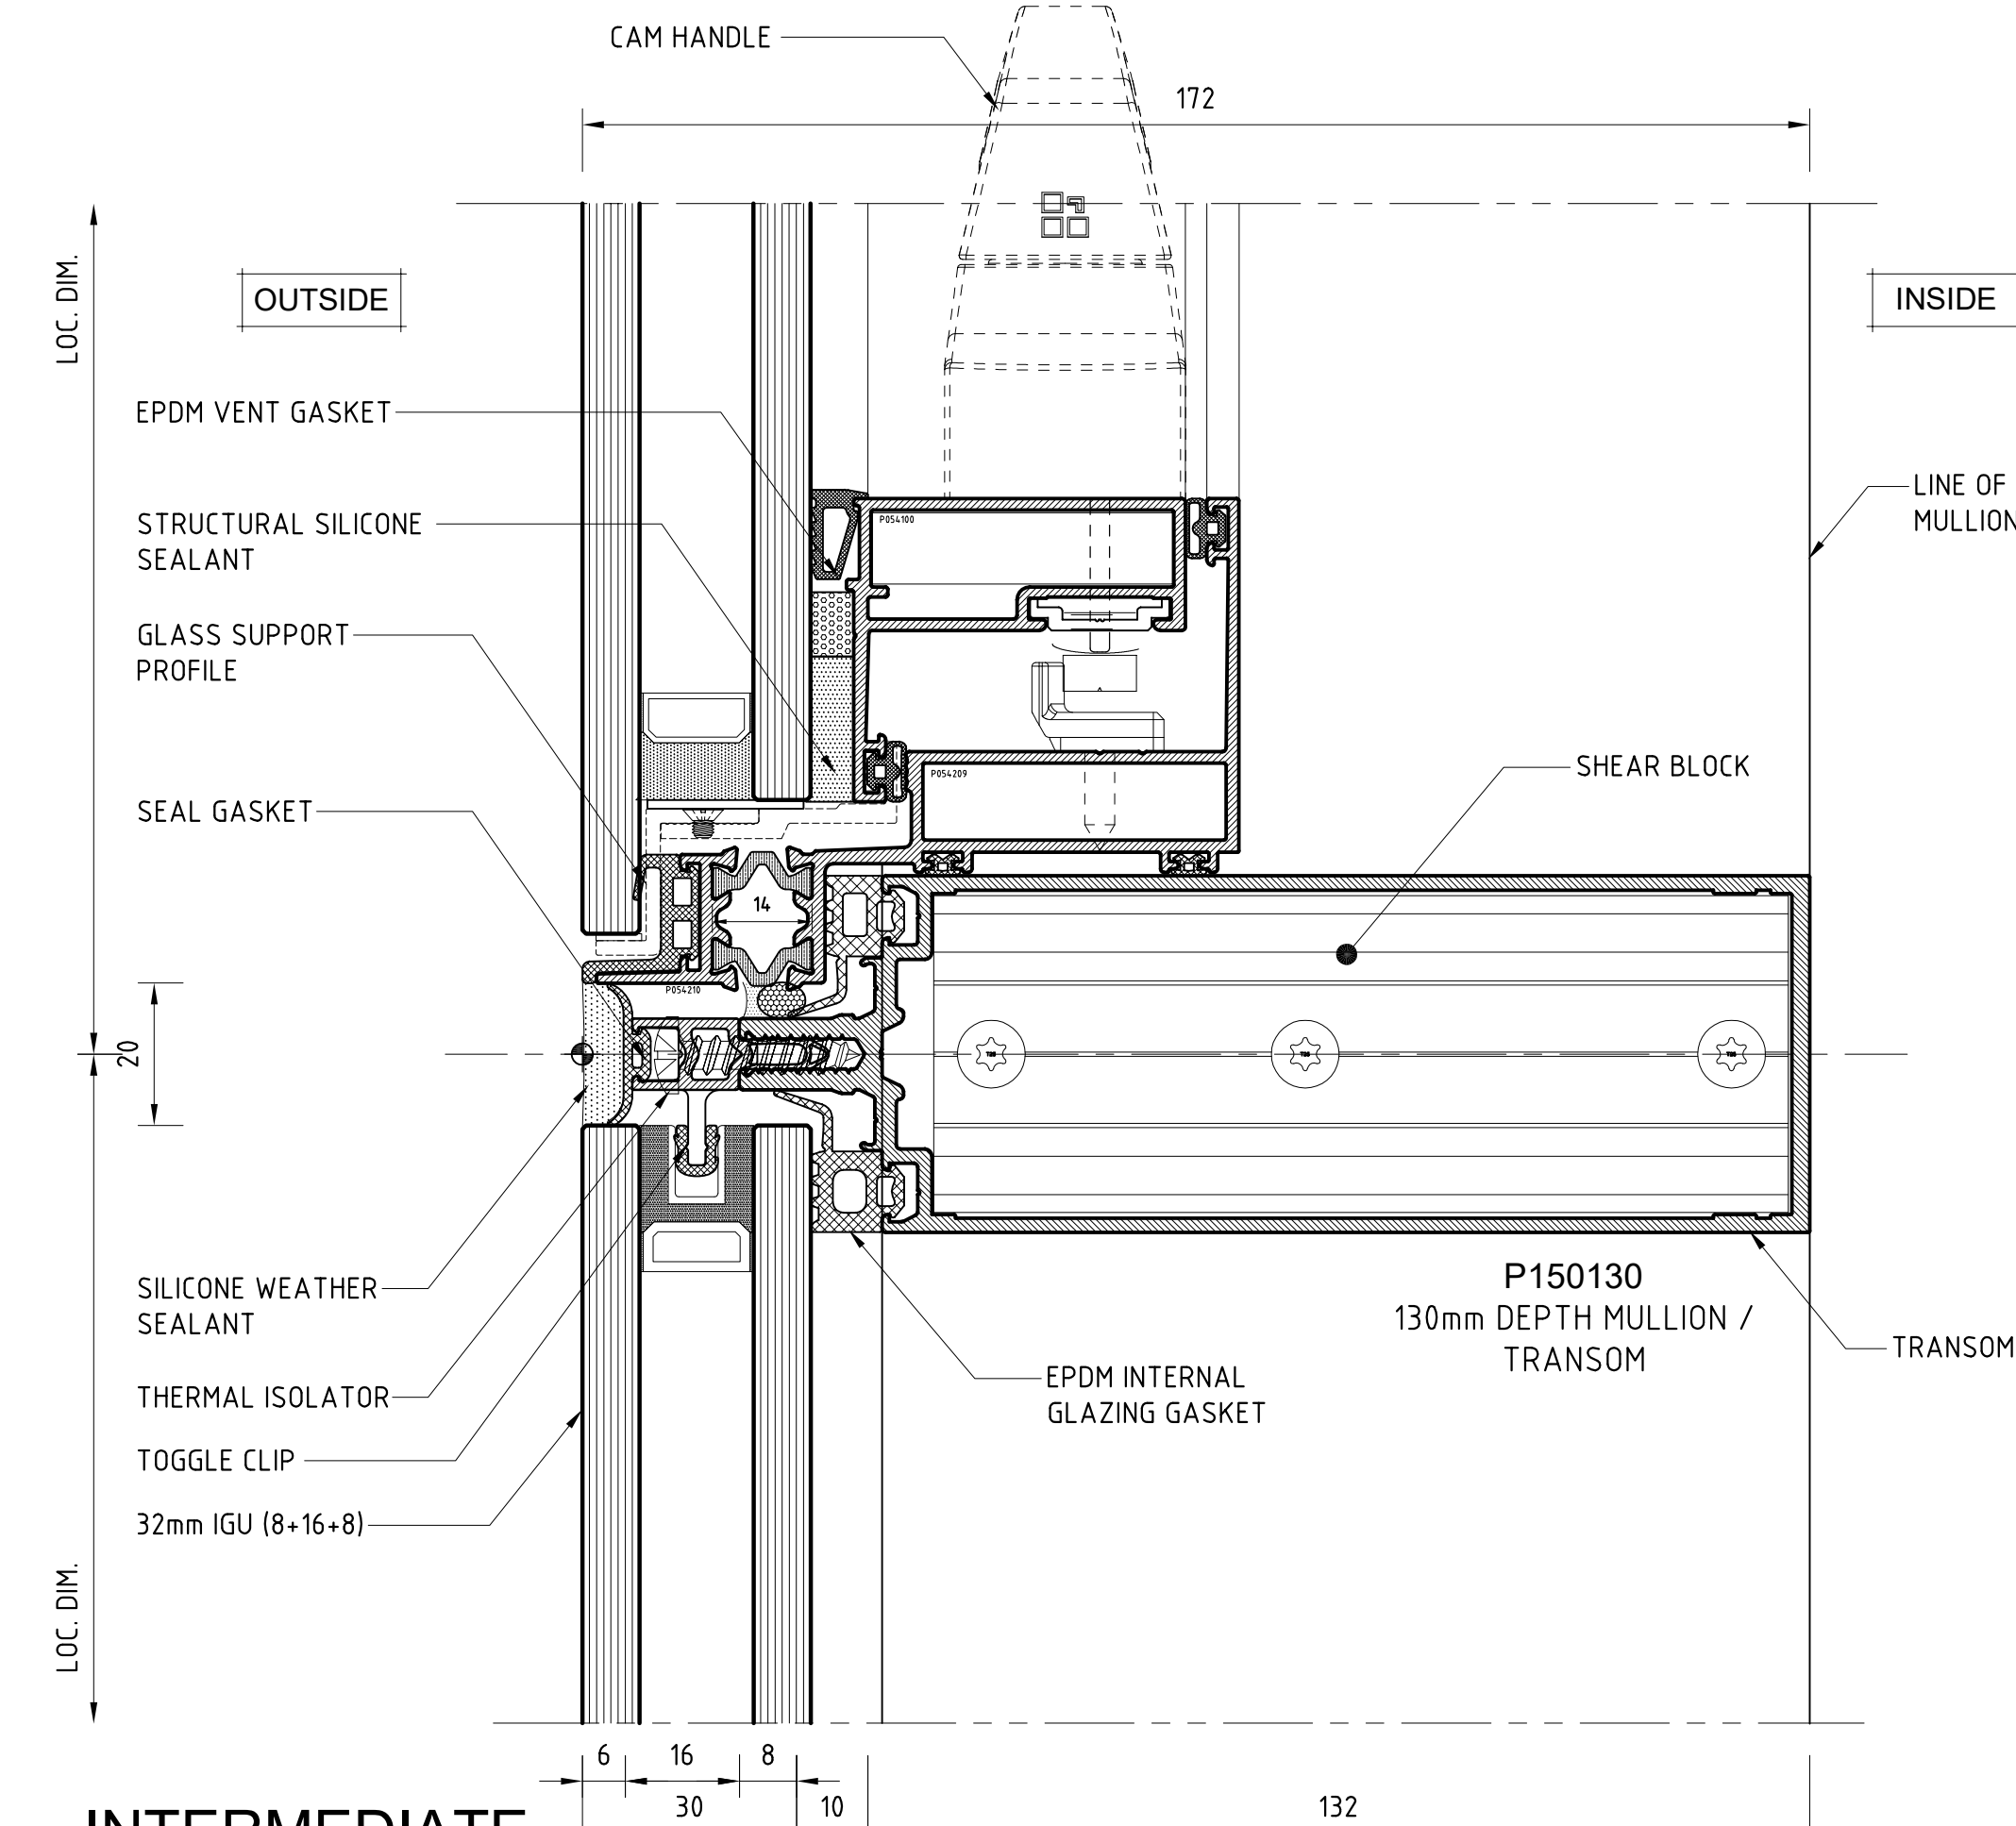

Project :

AJMAN CREEK TOWERS , Rashidia 01, Ajman U.A.E.

Consultant :

 CANADIAN
CONSULTANT

Client :

Mr. Ghaleb Kamel Jaber

support@sykon.ae
www.sykon.ae

